המבצע אחראי לבדיקת המידות ולהתאמתן במקום.
על המבצע לבקר את כל המידות ועל כל טעות או אי התאמה יודיע למתכנן.
אין לבצע מידות ע"פ מדידה מהשרטוט.

מקרא:

בטון ממשיך	▨
בטון מפסיק	▭
בטון צומח	▨
חתך מקומי	▒

הפצה:

שם	תאריך	

שינויים:

מהדורה	תאריך	תאור עדכון
00	11.12.25	

הערות כלליות:

1. אין לבצע ללא היתר בניה מאושר כדין. ביצוע וקידום עבודות יהיה רק בפיקוח מהנדס צמוד ובנוכחות מנהל עבודה מוסמך ורשום.
2. בהיעדר הנחיה אחרת- סוג הבטון יהיה ב-30 לפחות.
3. יש לקרוא תכנית זו יחד עם תכניות אדריכלות ושאר היועצים.
4. על הקבלן להודיע למתכנן על כל סטייה ו/או אי הבנה שלתכנית זו טרם הביצוע.
5. על הקבלן לשמור היטב על דרישות, על פי כל דין, בטיחות
מחמירות במהלך ביצוע העבודות. אין לבצע הרכבות של אלמנטים ו/או הנפות באזור בו עוברים אנשים. עמודים יתמכו ב-2 כיוונים.
7. יש לבצע בדיקות בטון (לחיצה) על פי דרישות הת"י ב- 7, 28, 60 יום, במבני מים יש לקחת דגימות לבדיקות מים ע"פ ת"י.
8. שרוולים ומעברים יש לקבל מיועצי חשמל, אינס' ומיזוג.
9. שים לב: בכל השטחים הרטובים כגון:
מרפסות שמש -חדרים רטובים -חיפויי חוץ -ספים וכו, יש לאטום ע"פ חוק תכנון ובניה.
10. גמר הבטון יהיה לפי תכניות אדריכליות, רצפות בטון יוחלקו בהליקופטר, שכבת שחיקה לפי הנחייה פרטנית של המתכנן והמזמין, גמר רמפות בטון יהיה, בהיעדר הנחייה אחרת, מסורק.
11. יש לתמוך את התקרה באזורים של הטרנספורמציה עד גמר התקשות הקומה שמעל.
12. עובי כיסוי הבטון ברכיבים הנמצאים מתחת לפני הקרקע יהיה 50 מ"מ.
13. עובי כיסוי הבטון ברכיבים הנמצאים מעל לפני הקרקע יהיה 30 מ"מ.
14. הבטון יתאים לדרגת חשיפה 3 לפי טבלה 3.2 בת"י 466 חלק 1.
15. סוג הפלדה: Φ_w - ת"י 4466 חלק 3.
$\overline{\Phi}$ - ת"י 4466 חלק 4.
16. התכניות לביצוע לאחר אישור אדריכל ויועץ קרקע.

תבנית
1:50

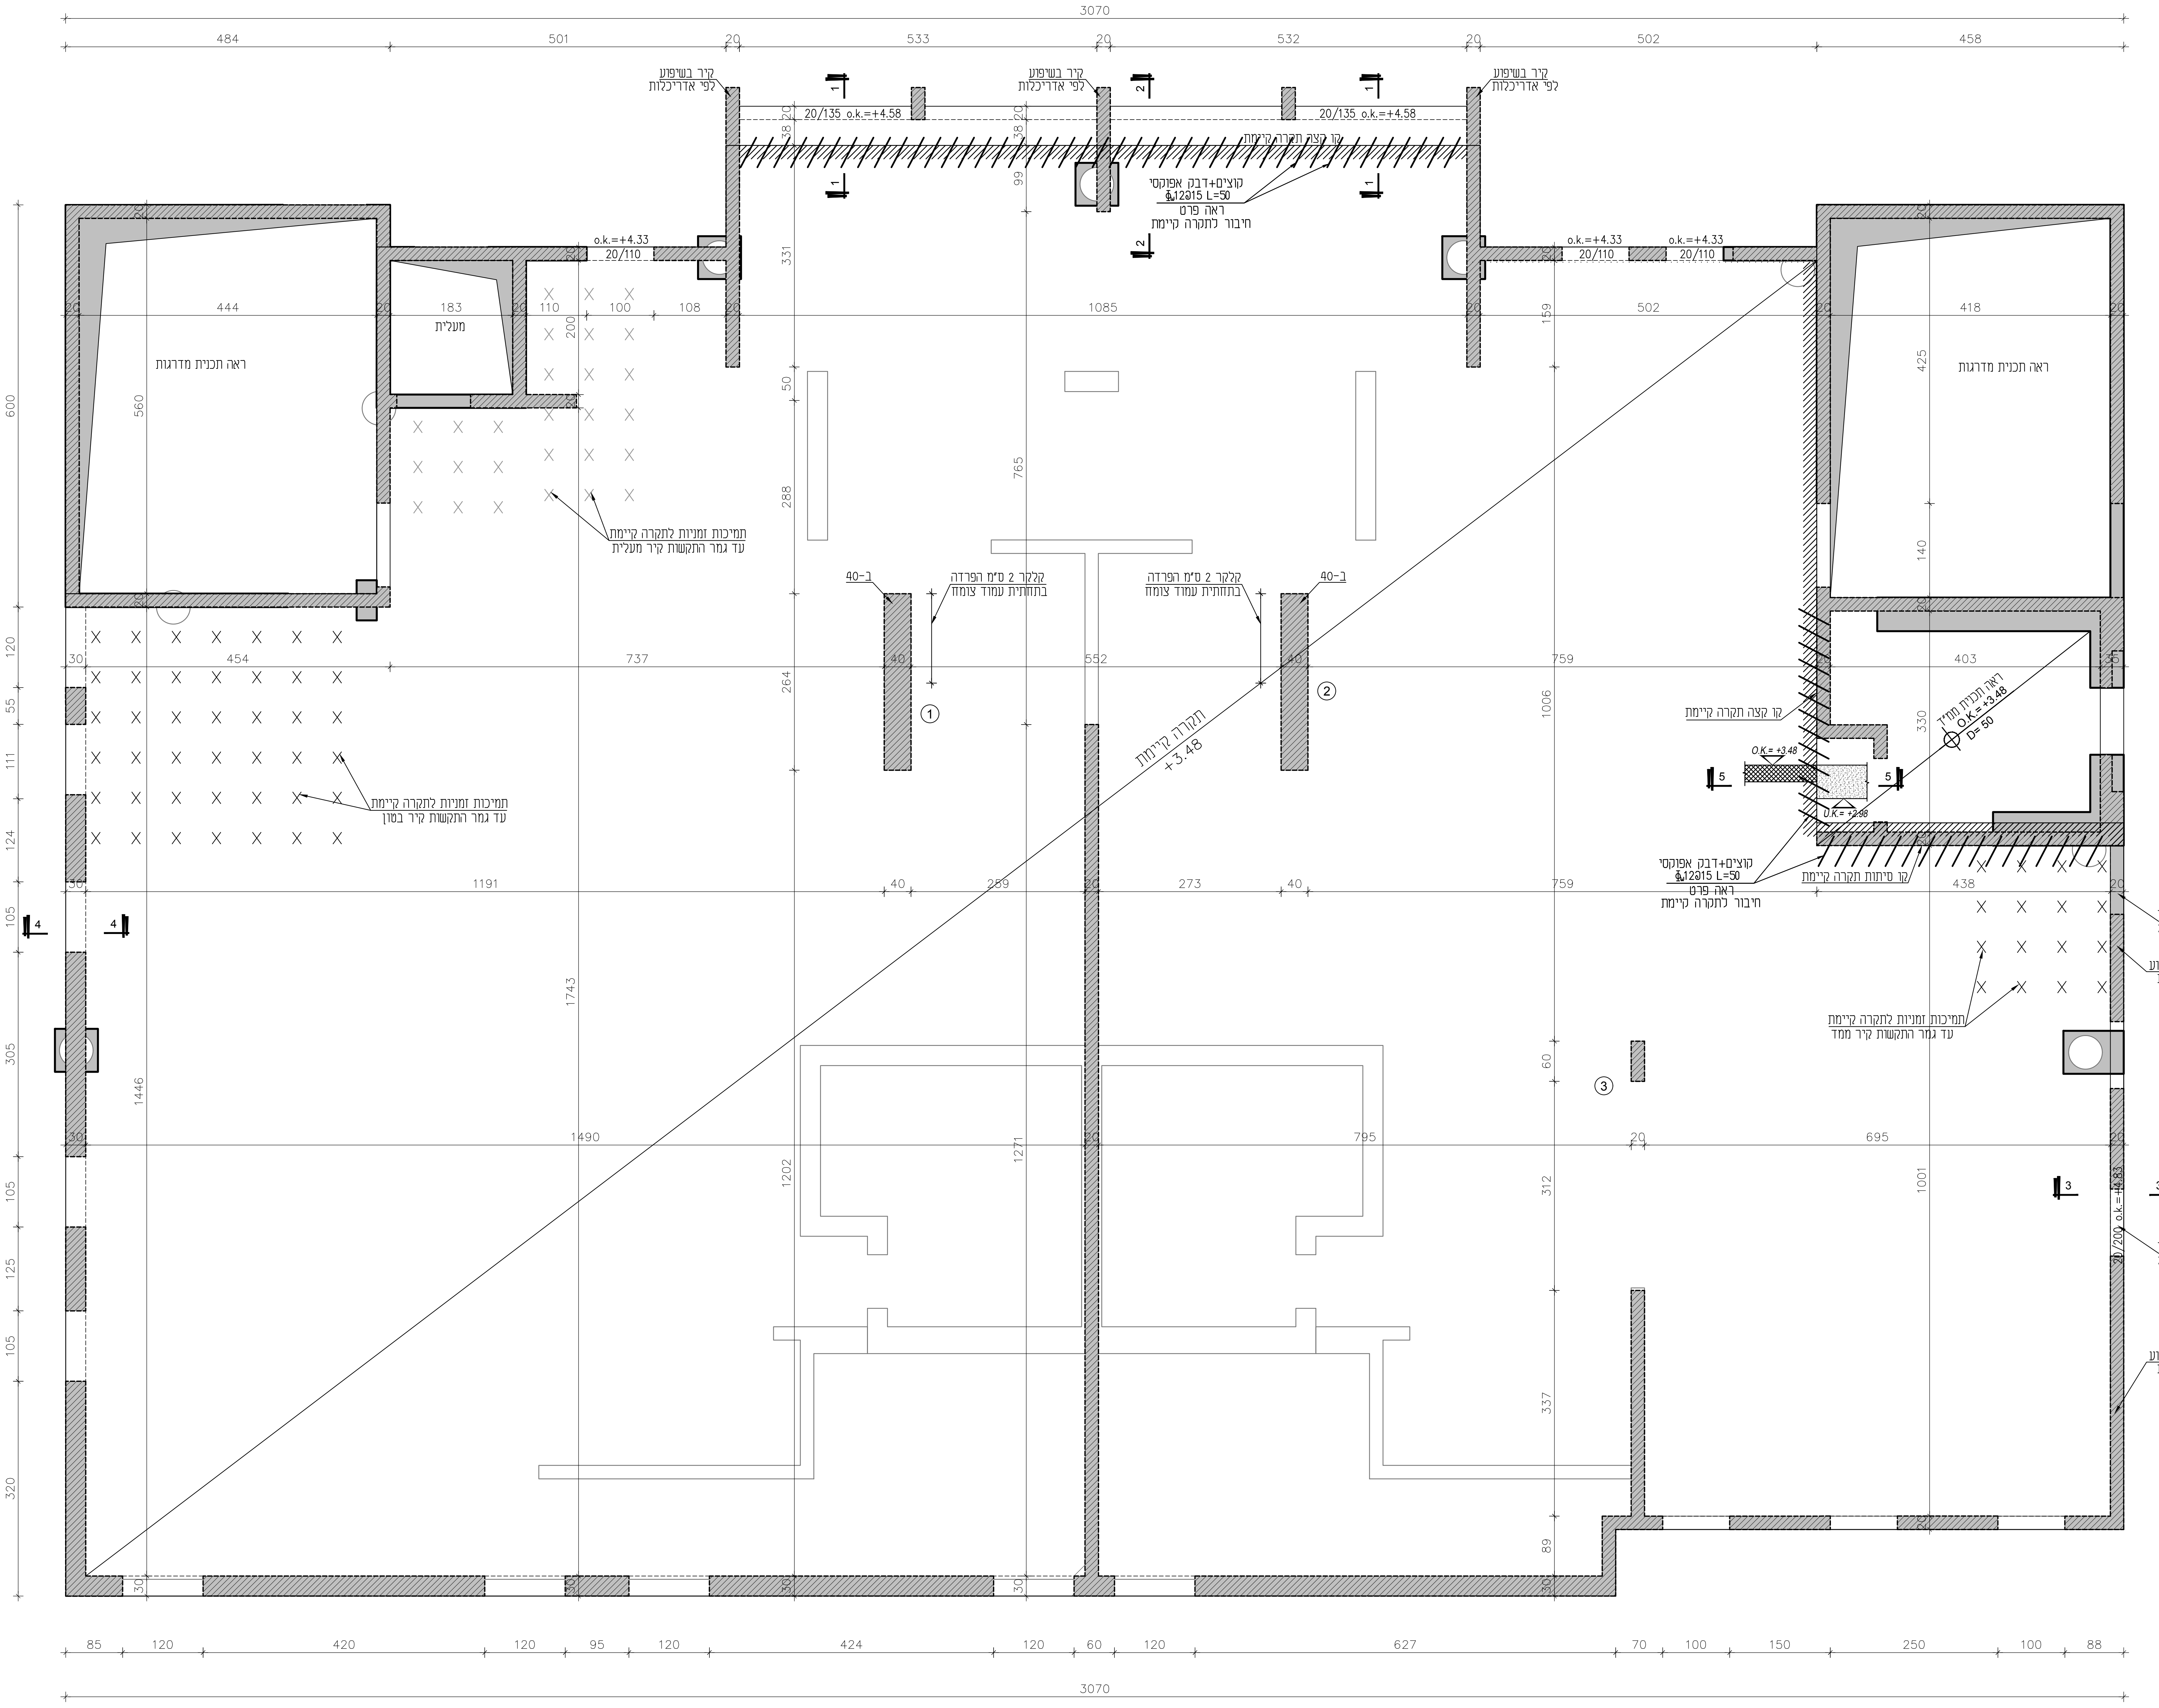
3070
484
501
20
533
20
532
20
502
458
קיר בשיפוע לפי אדריכלות
קיר בשיפוע לפי אדריכלות
קיר בשיפוע לפי אדריכלות
20/135 o.k.=+4.58
20/135 o.k.=+4.58
קו קצה תקרה קיימת
קוצים+דבק אפוקסי
Φw12@15 L=50
ראה פרט
חיבור לתקרה קיימת
o.k.=+4.33
20/110
o.k.=+4.33
20/110
o.k.=+4.33
20/110
1
2
444
183
110
100
108
1085
502
418
מעלית
ראה תכנית מדרגות
ראה תכנית מדרגות
600
560
331
99
38
200
50
288
765
159
425
140
תמיכות זמניות לתקרה קיימת
עד גמר התקשות קיר מעלית
ב-40
קלקר 2 ס"מ הפרדה
בתחתית עמוד צומח
ב-40
קלקר 2 ס"מ הפרדה
בתחתית עמוד צומח
120
30
454
737
552
759
403
35
55
111
124
264
1006
330
①
②
תקרה קיימת
+3.48
ראה תכנית ממ"ד
O.K.=+3.48
D=50
קו קצה תקרה קיימת
O.K.=+3.48
U.K.=+2.98
5
תמיכות זמניות לתקרה קיימת
עד גמר התקשות קיר בטון
קוצים+דבק אפוקסי
Φw12@15 L=50
ראה פרט
חיבור לתקרה קיימת
קו סיתות תקרה קיימת
1191
40
259
20
273
40
759
438
105
4
סיתות קורה קיימת
ללא פגיעה בברזל הקיים
ויציקת קורה חדשה 20/200
קיר בשיפוע
ראה חזית
תמיכות זמניות לתקרה קיימת
עד גמר התקשות קיר ממד
305
1743
1446
60
③
1490
1271
1202
795
20
695
312
1001
3
20/200 o.k.=+4.83
סיתות קורה קיימת
ללא פגיעה בברזל הקיים
ויציקת קורה חדשה 20/200
105
125
105
337
קיר בשיפוע
ראה חזית
320
89
30
85
120
420
120
95
120
424
120
60
120
627
70
100
150
250
100
88
3070

חתך 5-5
1:25

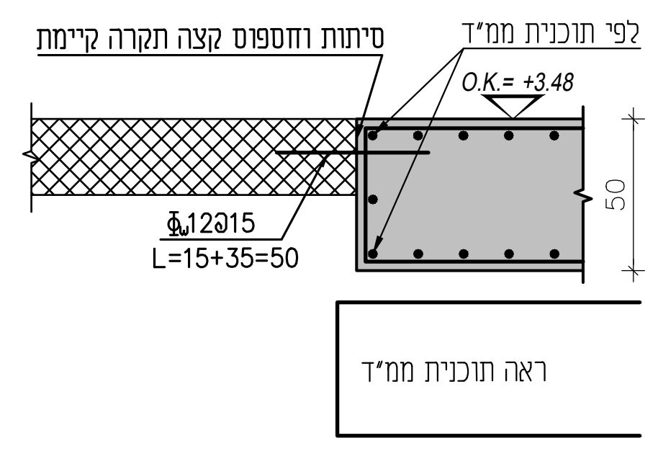
סיתות וחספוס קצה תקרה קיימת
לפי תוכנית ממ"ד
O.K.= +3.48
Φw12@15
L=15+35=50
50
ראה תוכנית ממ"ד

חתך 4-4
1:25

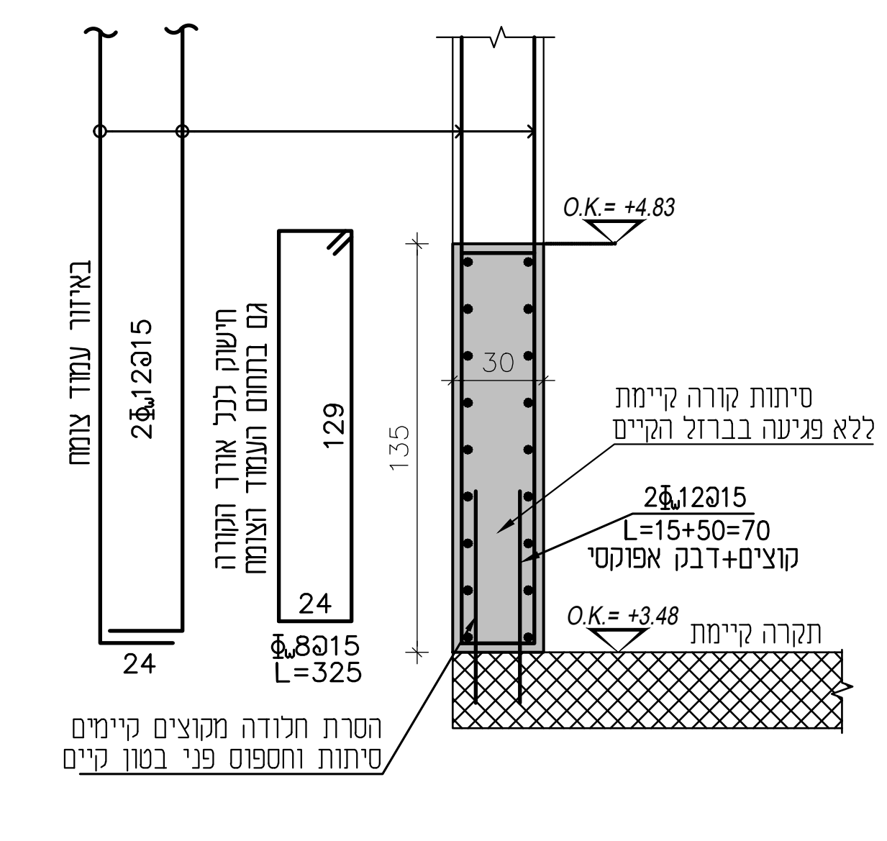
באיזור עמוד צומח
2Φw12@15
24
חישוק לכל אורך הקורה גם בתחום העמוד הצומח
129
24
Φw8@15
L=325
135
30
O.K.= +4.83
סיתות קורה קיימת
ללא פגיעה בברזל הקיים
2Φw12@15
L=15+50=70
קוצים+דבק אפוקסי
O.K.= +3.48
תקרה קיימת
הסרת חלודה מקוצים קיימים
סיתות וחספוס פני בטון קיים

חתך 3-3
1:25

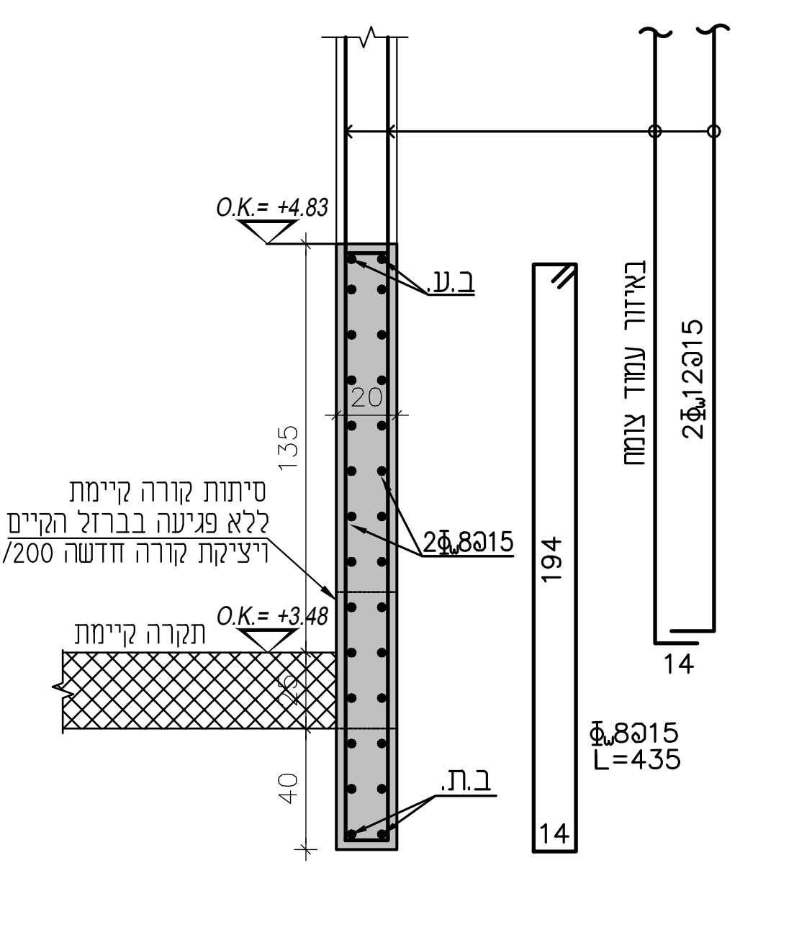
O.K.= +4.83
ב.ע.
20
135
סיתות קורה קיימת
ללא פגיעה בברזל הקיים
ויציקת קורה חדשה 20/200
2Φw8@15
O.K.= +3.48
תקרה קיימת
40
ב.ת.
194
14
Φw8@15
L=435
באיזור עמוד צומח
2Φw12@15
14

חתך 2-2
1:25

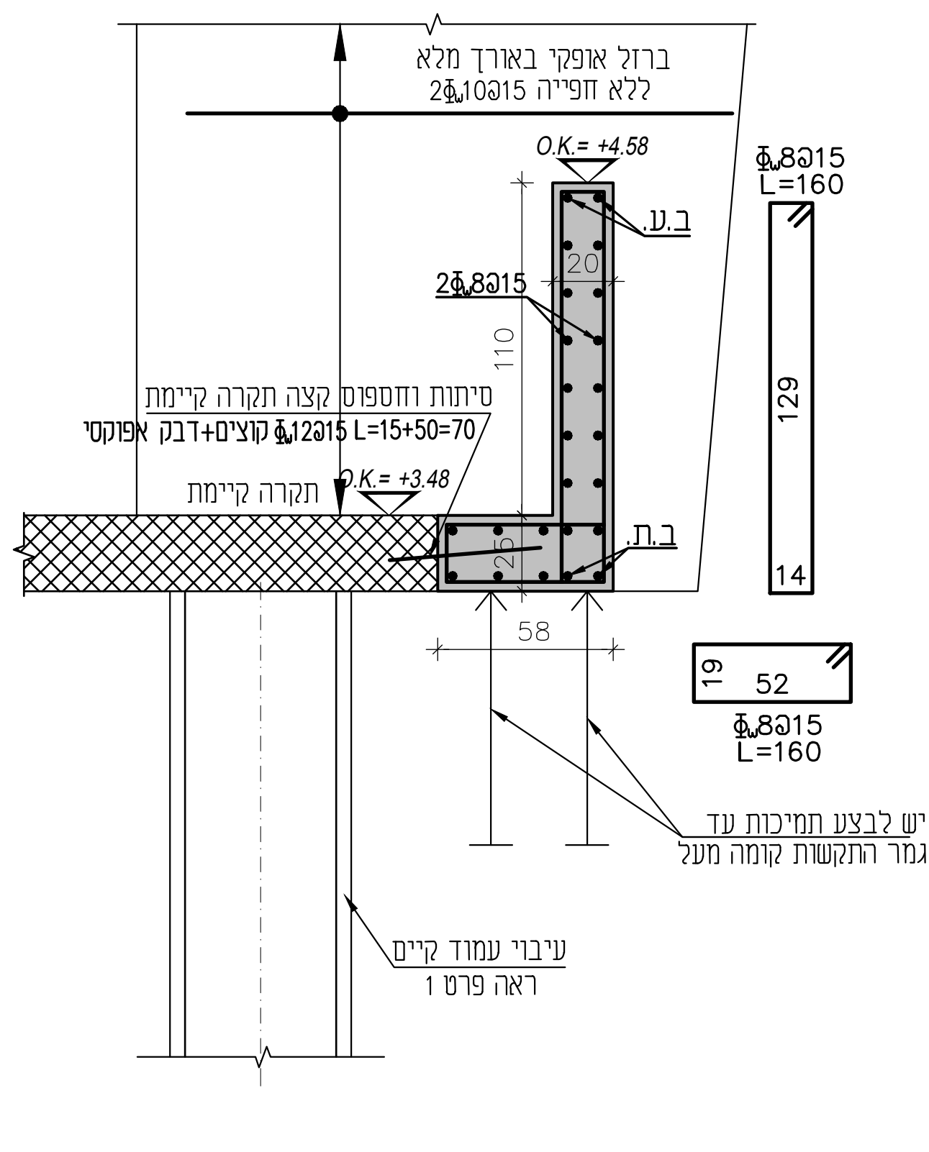
ברזל אופקי באורך מלא
2Φw10@15 ללא חפייה
O.K.= +4.58
ב.ע.
20
2Φw8@15
110
סיתות וחספוס קצה תקרה קיימת
Φw12@15 L=15+50=70 קוצים+דבק אפוקסי
O.K.= +3.48
תקרה קיימת
25
ב.ת.
58
Φw8@15
L=160
129
14
19
52
Φw8@15
L=160
יש לבצע תמיכות עד
גמר התקשות קומה מעל
עיבוי עמוד קיים
ראה פרט 1

חתך 1-1
1:25

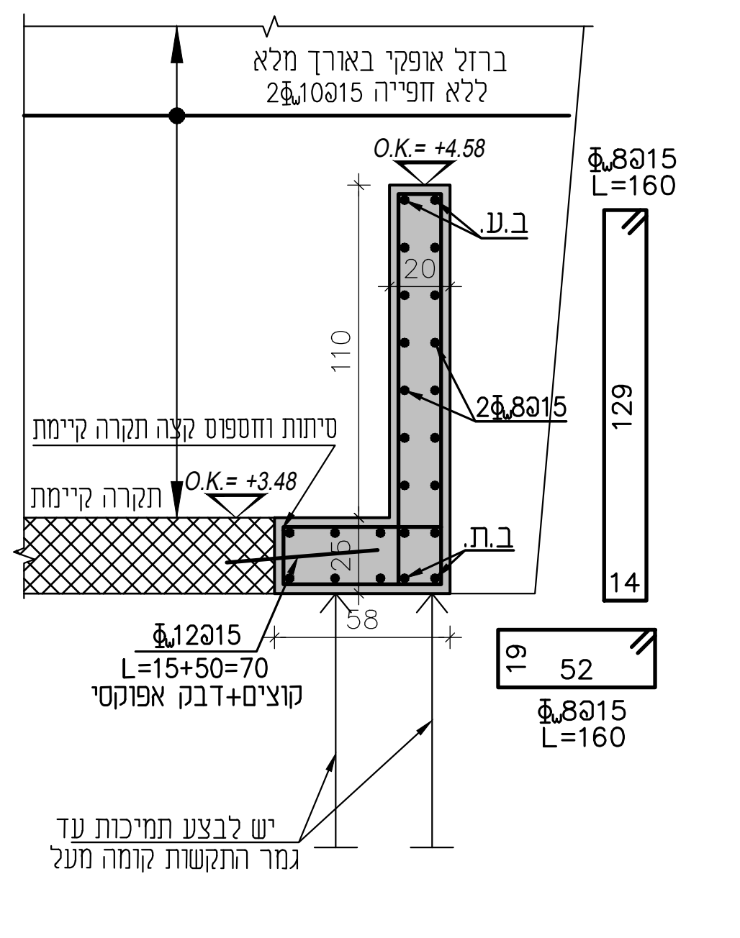
ברזל אופקי באורך מלא
2Φw10@15 ללא חפייה
O.K.= +4.58
ב.ע.
20
110
2Φw8@15
סיתות וחספוס קצה תקרה קיימת
O.K.= +3.48
תקרה קיימת
25
ב.ת.
58
Φw12@15
L=15+50=70
קוצים+דבק אפוקסי
Φw8@15
L=160
129
14
19
52
Φw8@15
L=160
יש לבצע תמיכות עד
גמר התקשות קומה מעל

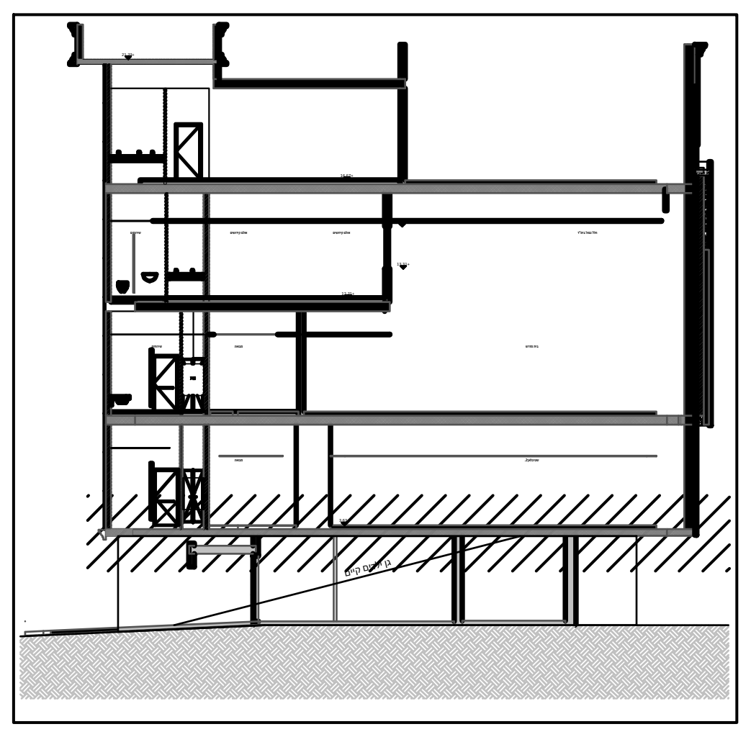

היזם
עמותת צרכי הרבים רצופות

אדריכלות
איבגי קרמן אדריכלות

שם הפרויקט :
בית כנסת הרמב"ם
מודיעין עילית

שם התכנית :
קומת קרקע
תבנית

סטטוס: ○ לעיון ○ לאישור ● למכרז ○ לביצוע

מהדורה:	תאריך:
00	11.12.2025

שם קובץ: 100-GWE-100 קנ"מ: 1:25 1:50
מס' גליון: 100-GWE-100-00 מס' סידורי: 000

פוליגון הנדסה
תכנון ייעוץ ופיקוח