טבלת עמודים
1:25

מספר עמוד	מידות חתך	ברזל אורכי	חישוק
1 2	40/264	2×4⌀20, 25⌀14; 40; 264	⌀12@10 L=330; ⌀12@10 L=290; ⌀12@10 L=330; 121; 101; 121; 34; 36; 34
3	20/60	4+4⌀14; 20; 60	⌀8@20<10> L=155; 14; 54; ⌀8@20<10>
5	20/160	9+9⌀16; 20; 160	⌀8@20<10> L=165; ⌀8@20<10> L=200; ⌀8@20<10> L=165; 60; 78; 60; 14; 14
6	20/150	8+8⌀16; 20; 150	⌀8@20<10> L=155; ⌀8@20<10> L=200; ⌀8@20<10> L=155; 55; 78; 55; 14
7	30/95	95; 30; 14⌀16	⌀8@20<10> L=155; 24; 89; 2⌀8@20<10>
9	30/125	16⌀16; 30; 125	⌀8@20<10> L=300; 24; 119; 2⌀8@20<10>
10	30/55	10⌀16; 30; 55	⌀8@20<10> L=165; 14; 49; ⌀8@20<10>
11	20/55	4+4⌀16; 20; 55	⌀8@20<10> L=145; 14; 49; ⌀8@20<10>
12		2⌀12@20	באזור ללא קורה: ⌀8@15; 14 — באיזור של קורה: ⌀12@15; 100; 100

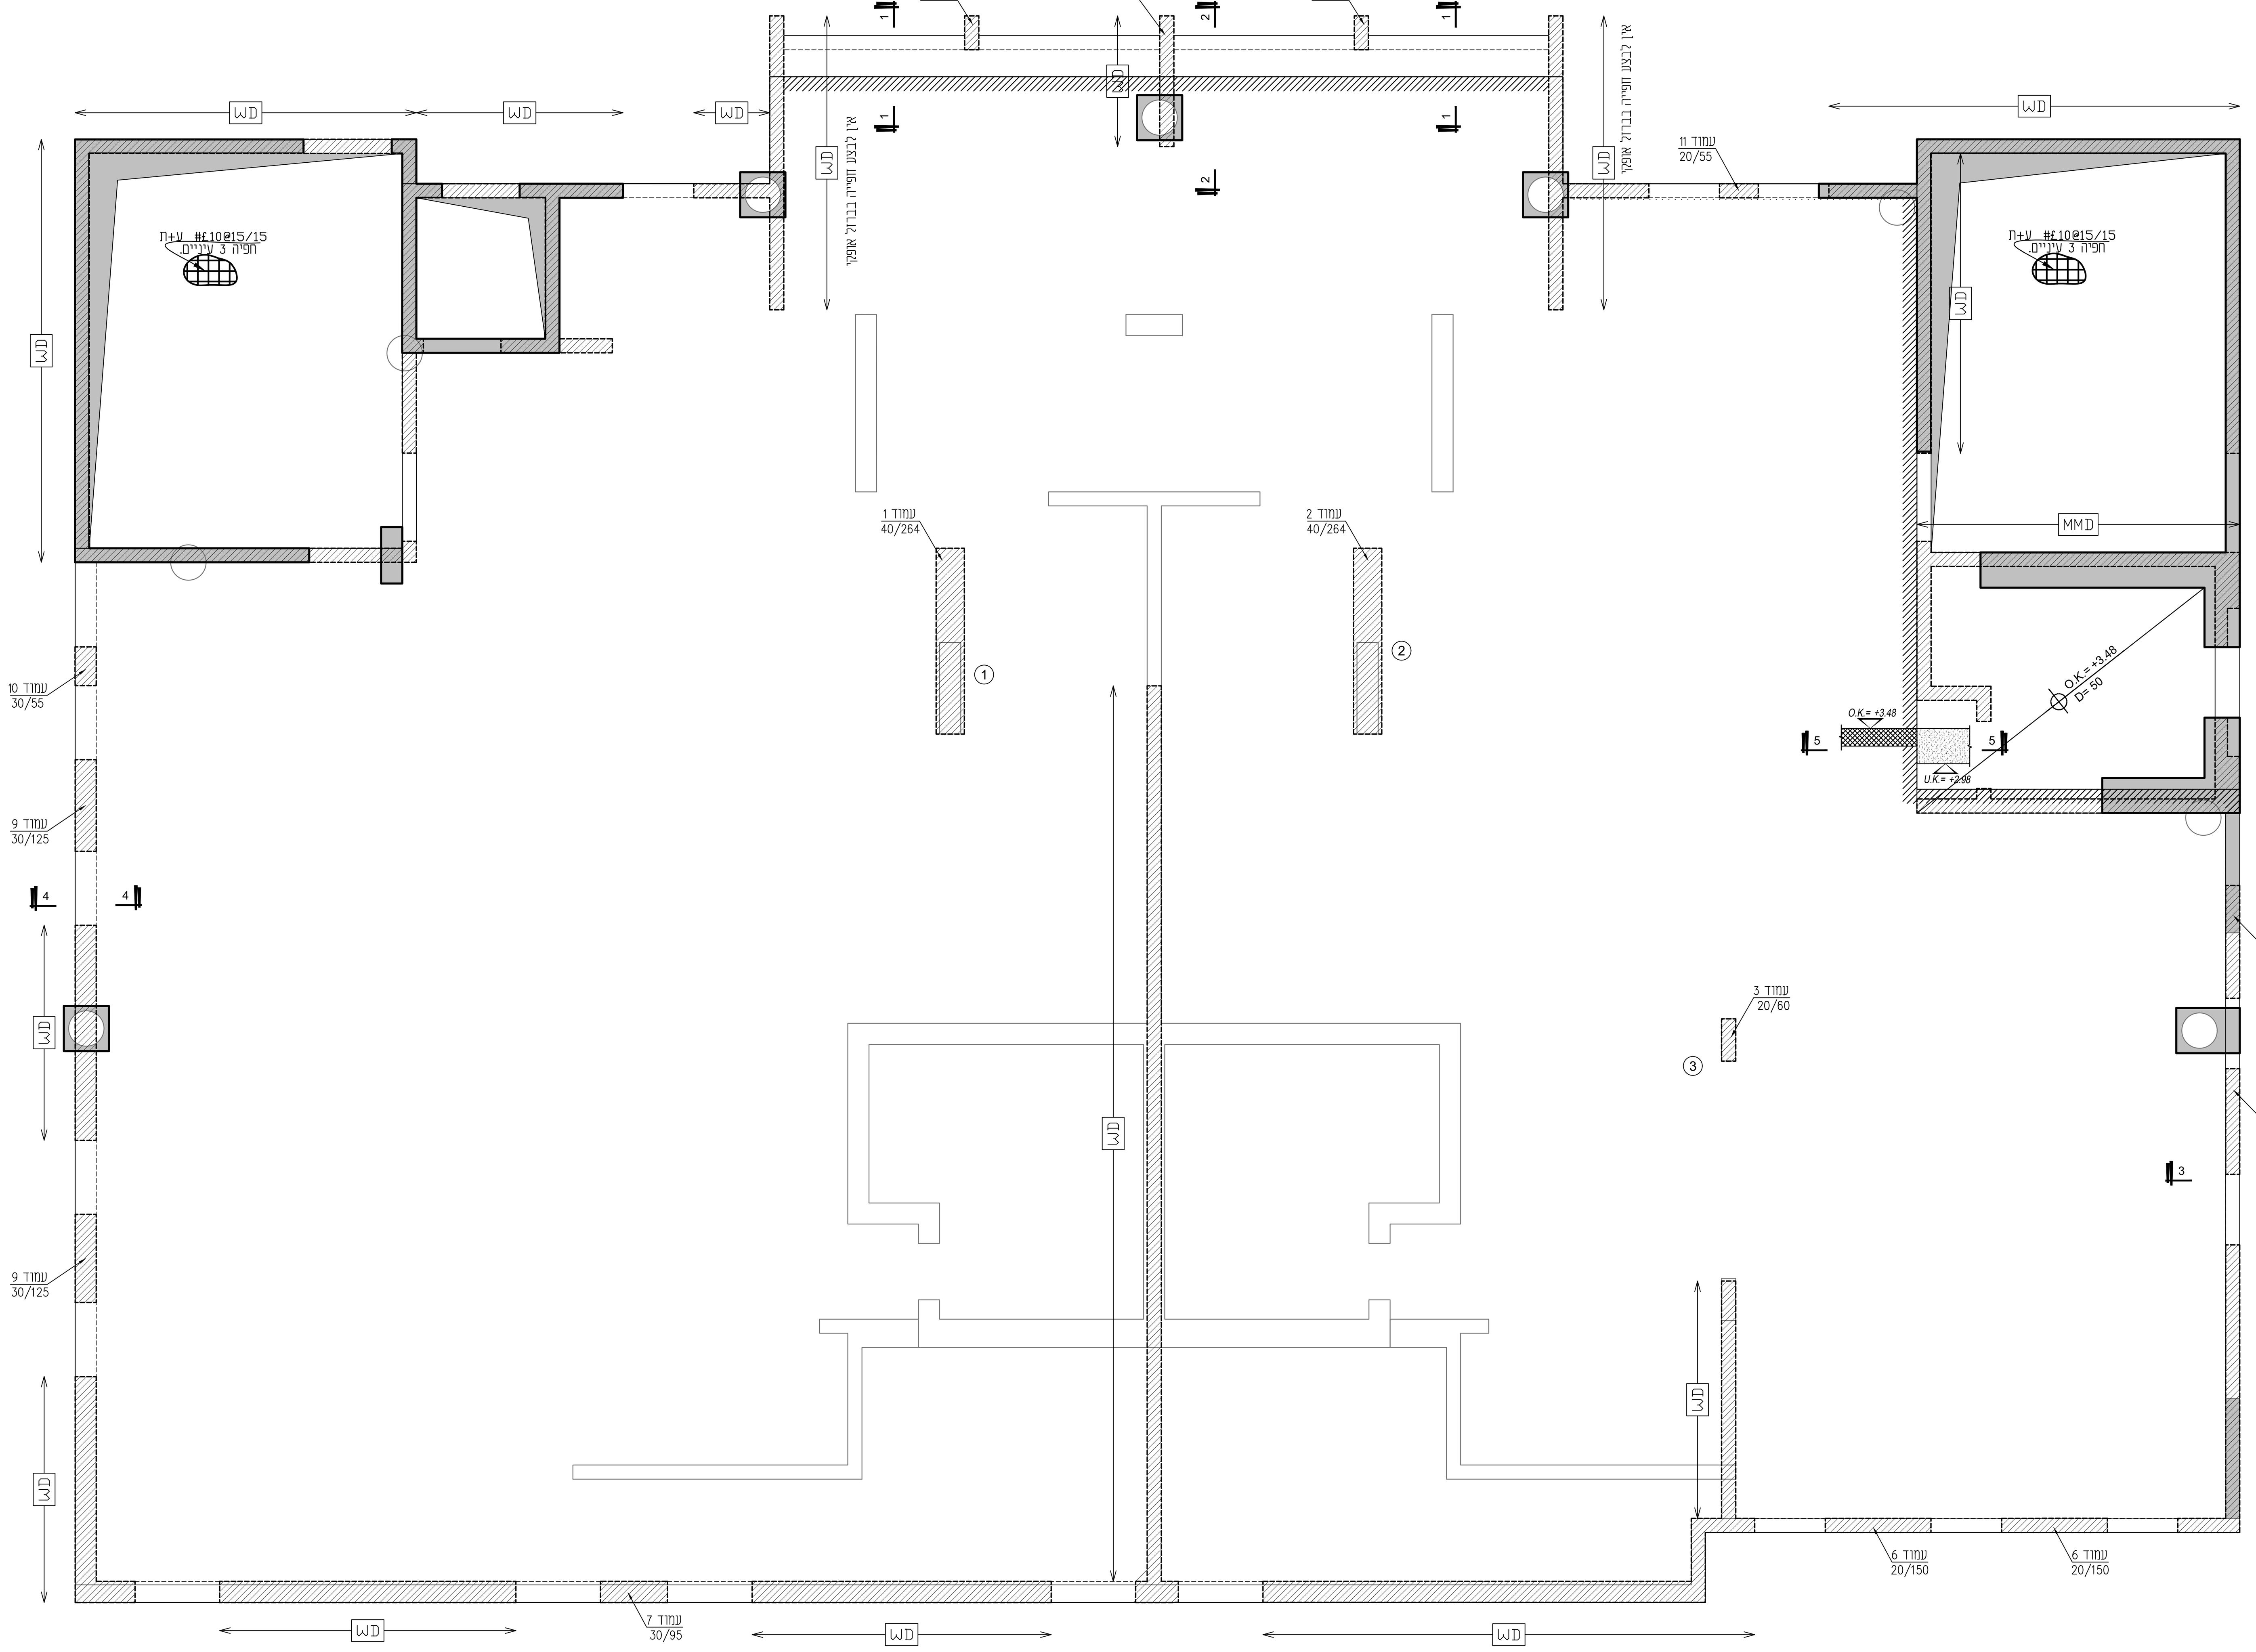

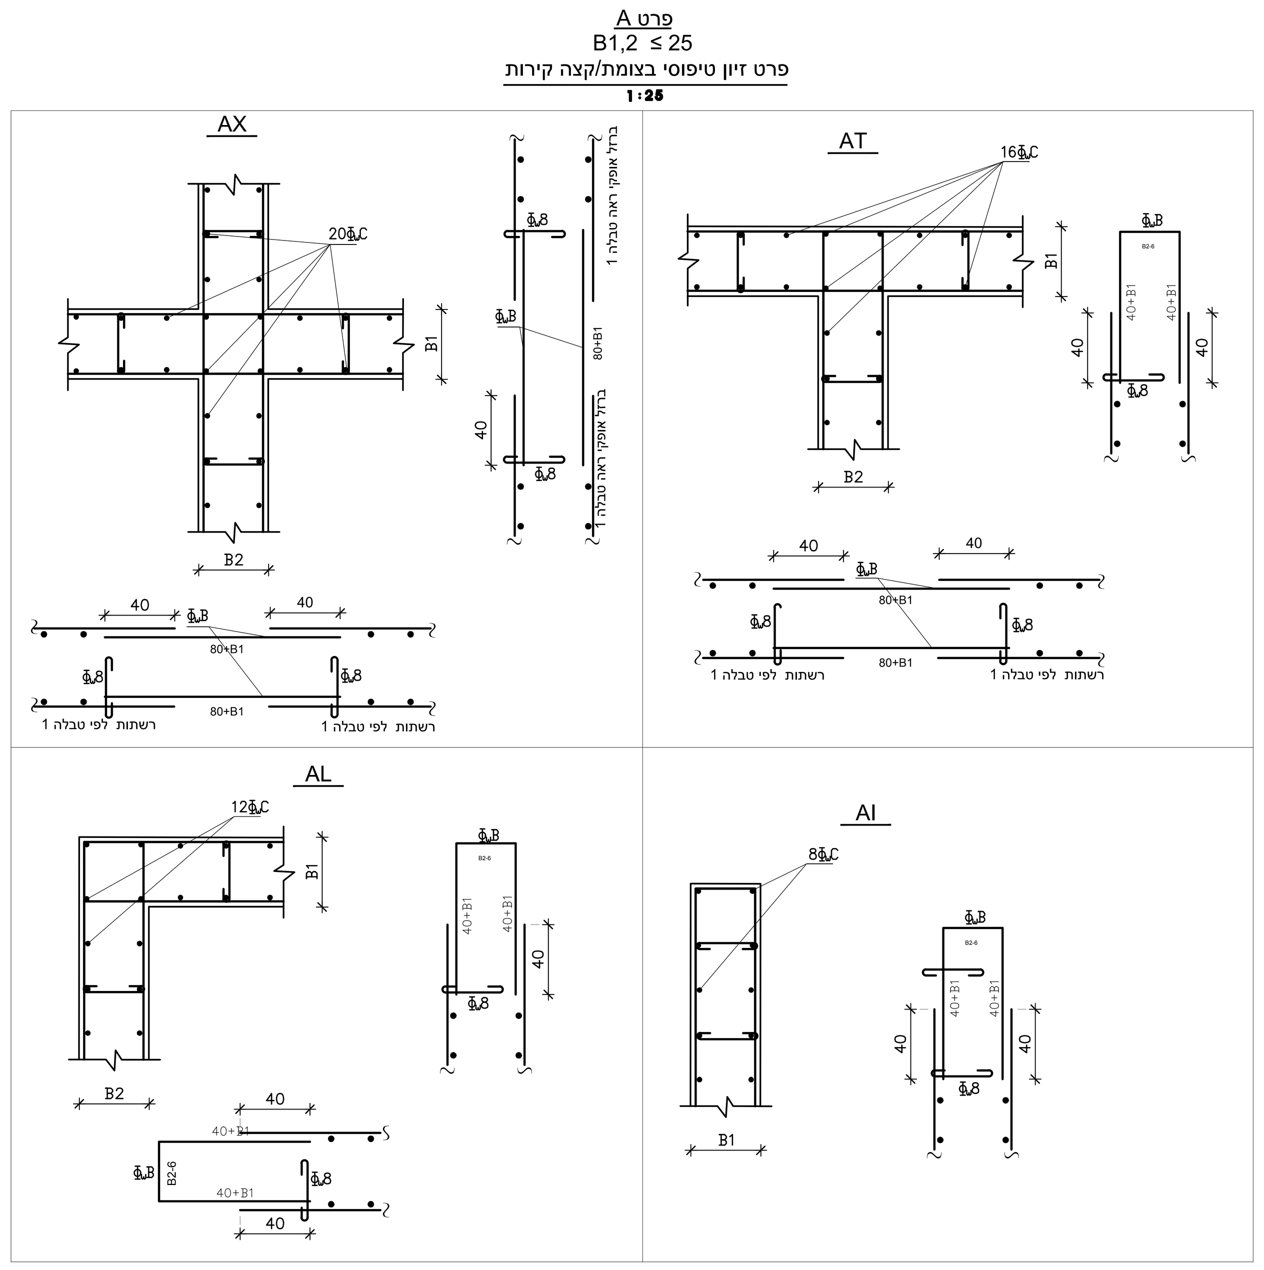

טבלת ברזל קירות

סימון הקיר	ברזל אנכי A	ברזל אופקי B	ברזל פינה אנכי C	סוג בטון
WD	2⌀12@15	2⌀10@15	ראה טבלה	ב-30
MMD	ראה תוכנית ממ"ד			

סוג צומת	C = קוטר ברזל
AX	⌀12
AT	⌀16
AL	⌀16
AI	⌀16

הערות:
- קלמרות בפסיעות לגובה בהתאם לברזל אופקי (ראה טבלה 1).
- הקבלן רשאי להגיש לאישור משרדנו סידור שונה העומד בסטנדרטים המקובלים ובתקינה.
- B קוטר זיון אופקי בקיר)ראה טבלה 1(

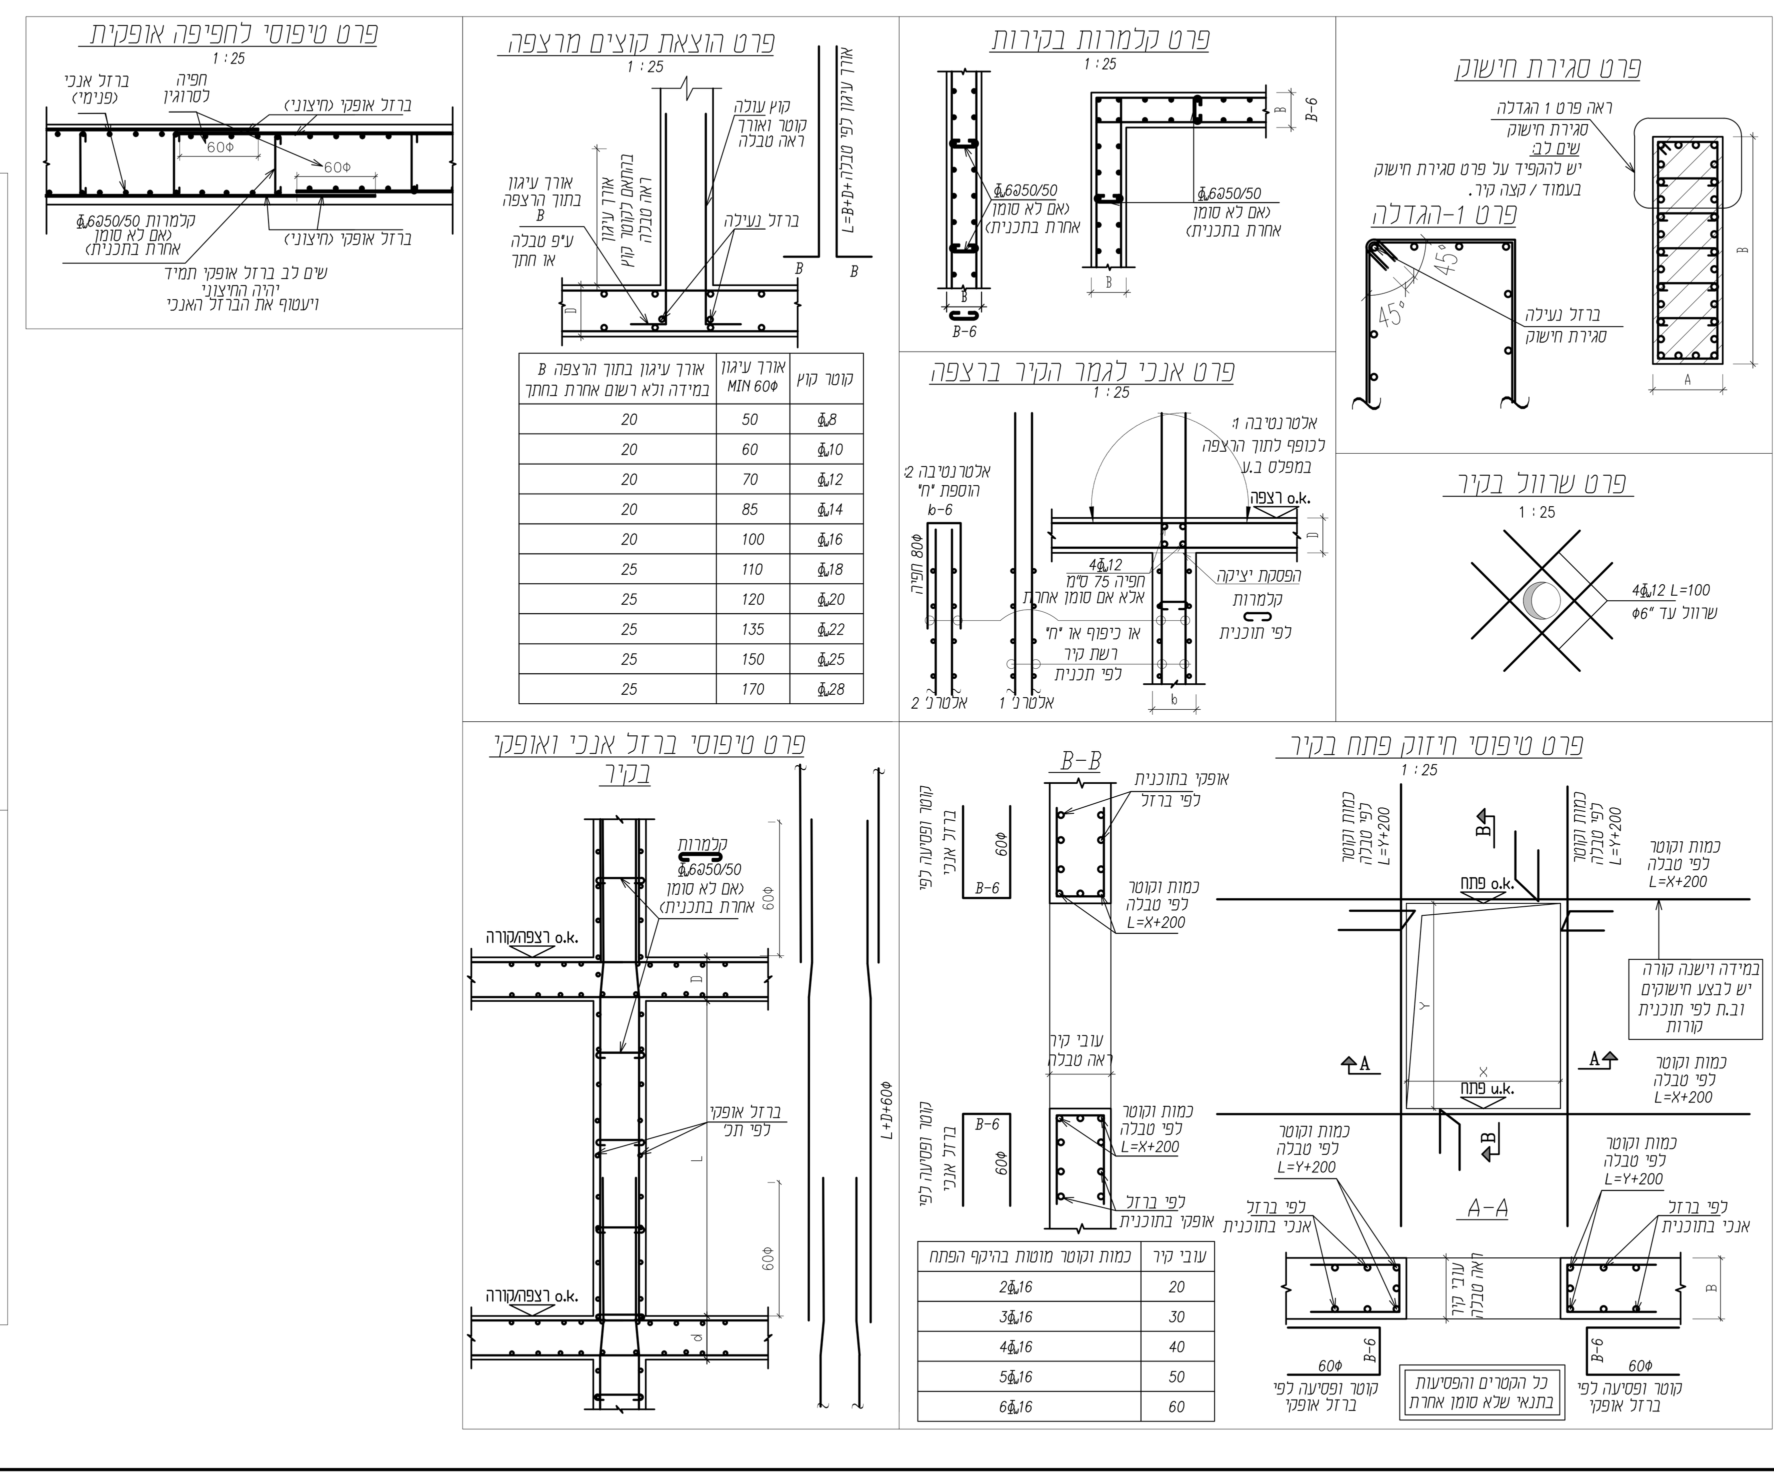

המבצע אחראי לבדיקת המידות ולהתאמתן במקום.
על המבצע לבקר את כל המידות ועל כל טעות או אי התאמה יודיע למתכנן.
אין לבצע מידות ע"פ מדידה מהשרטוט.

מקרא:

בטון ממשיך	
בטון מפסיק	
בטון צומח	
חתך מקומי	

הפצה:

שם	תאריך	

שינויים:

מהדורה	תאריך	תאור עדכון
00	11.12.25	

הערות כלליות:
1. אין לבצע ללא היתר בניה מאושר כדין. ביצוע וקידום עבודות יהיה רק בפיקוח מהנדס צמוד ובנוכחות מנהל עבודה מוסמך ורשום.
2. בהיעדר הנחיה אחרת- סוג הבטון יהיה ב-30 לפחות.
3. יש לקרוא תכנית זו יחד עם תכניות אדריכלות ושאר היועצים.
4. על הקבלן להודיע למתכנן על כל סטייה ו/או אי הבנה שבתכנית זו טרם הביצוע.
5. על הקבלן לשמור היטב על דרישות, על פי כל דין, בטיחות מחמירות במהלך ביצוע העבודות. אין לבצע הרכבות של אלמנטים ו/או הנפות באזור בו עוברים אנשים. עמודים יתמכו ב-2 כיוונים.
7. יש לבצע בדיקות בטון (לחיצה) על פי דרישות הת"י ב- 7, 28, 60 יום, במבני מים יש לקחת דגימות לבדיקות מים ע"פ ת"י.
8. שרוולים ומעברים יש לקבל מיועצי חשמל, אינס' ומיזוג.
9. שים לב: בכל השטחים הרטובים כגון: מרפסות שמש -חדרים רטובים -חיפויי חוץ -ספים וכו, יש לאטום ע"פ חוק תכנון ובניה.
10. גמר הבטון יהיה לפי תכניות אדריכליות, רצפות בטון יוחלקו בהליקופטר, שכבת שחיקה לפי הנחייה פרטנית של המתכנן והמזמין, גמר רמפות בטון יהיה, בהיעדר הנחייה אחרת, מסורק.
11. יש לתמוך את התקרה באזורים של הטרנספורמציה עד גמר התקשות הקומה שמעל.
12. עובי כיסוי הבטון ברכיבים הנמצאים מתחת לפני הקרקע יהיה 50 מ"מ.
13. עובי כיסוי הבטון ברכיבים הנמצאים מעל לפני הקרקע יהיה 30 מ"מ.
14. הבטון יתאים לדרגת חשיפה 3 לפי טבלה 3.2 בת"י 466 חלק 1.
15. סוג הפלדה: ⌀ – ת"י 4466 חלק 3.
⌶ – ת"י 4466 חלק 4.
16. התכניות לביצוע לאחר אישור אדריכל ויועץ קרקע.

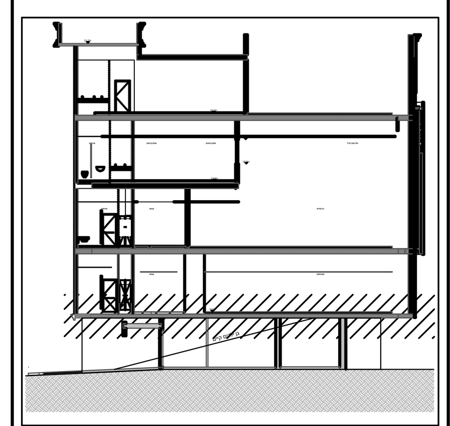

היזם
עמותת צרכי הרבים רצופות

אדריכלות
איבגי קרמן אדריכלות

שם הפרויקט :
בית כנסת הרמב"ם
מודיעין עילית

שם התכנית :
קומת קרקע
ברזל קירות ועמודים

סטטוס:	לעיון ○	לאישור ○	למכרז ○	לביצוע ○

מהדורה:	תאריך:
00	11.12.2025
שם קובץ: 100-GWE-100	קנ"מ: 1:25 1:50
מס' גליון: 100-GWE-100-rw-00	מס' סידורי: 000

פוליגון הנדסה
תכנון ייעוץ ופיקוח