תבנית
1:50

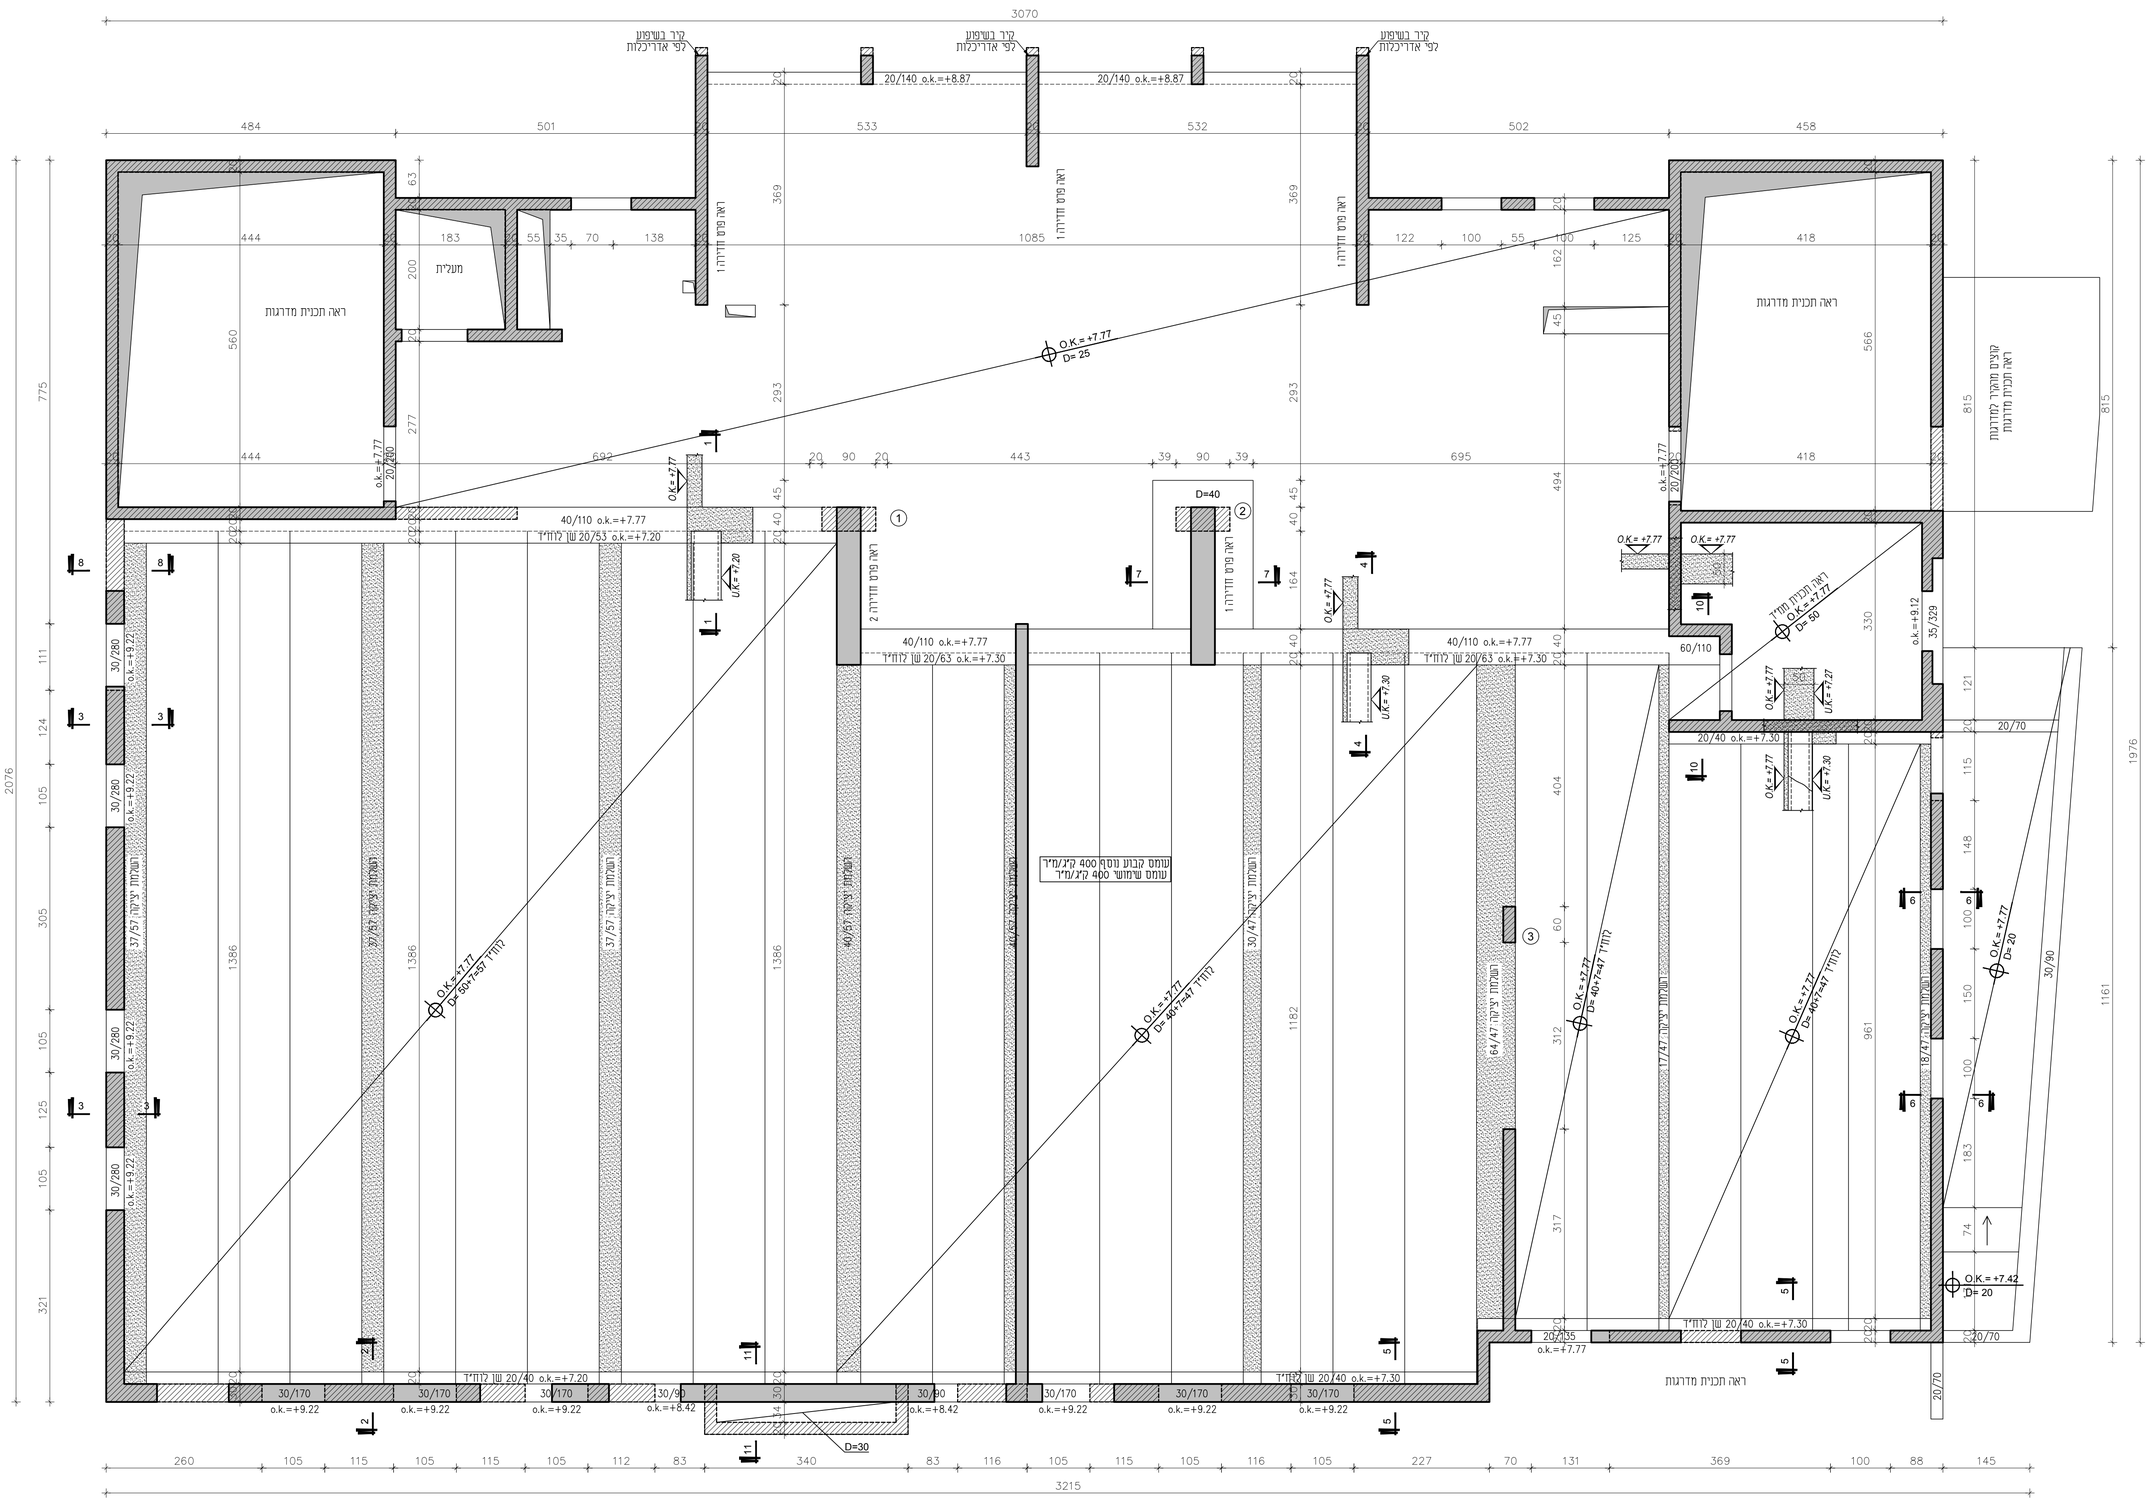

חתך 1-1
1:25

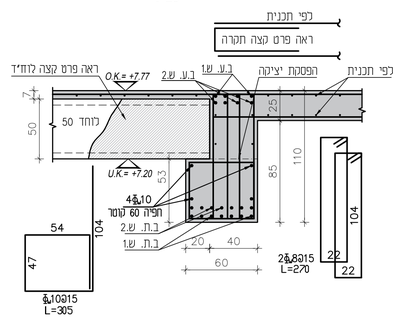

חתך 2-2
1:25

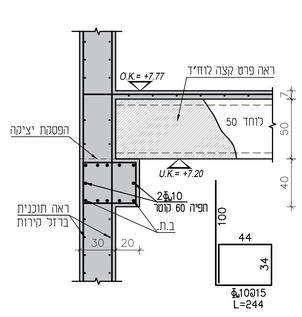

חתך 3-3
1:25

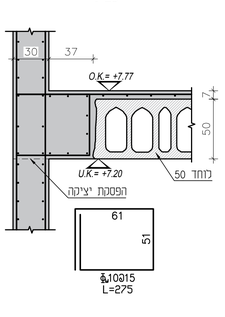

חתך 4-4
1:25

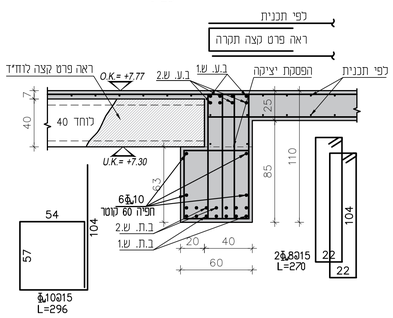

חתך 5-5
1:25

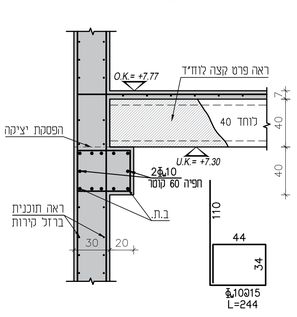

חתך 6-6
1:25

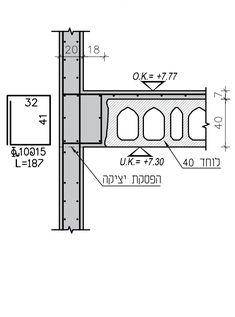

חתך 7-7
1:25

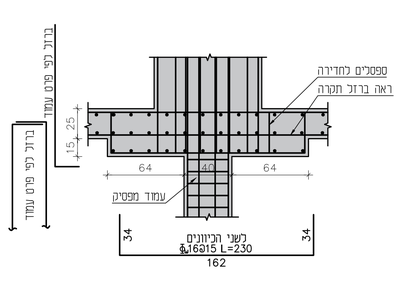

חתך 8-8
1:25

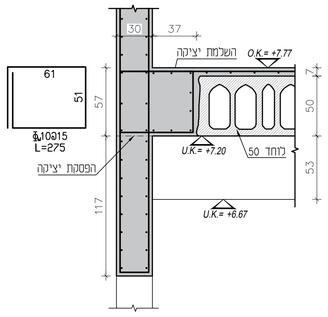

חתך 10-10
1:25

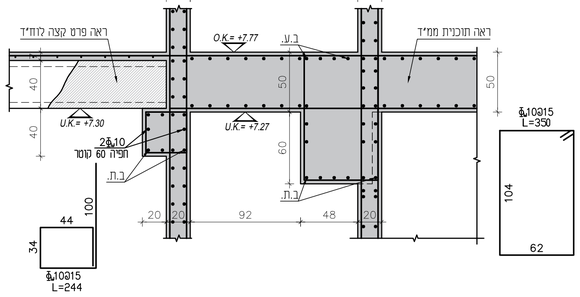

חתך 11-11
1:25

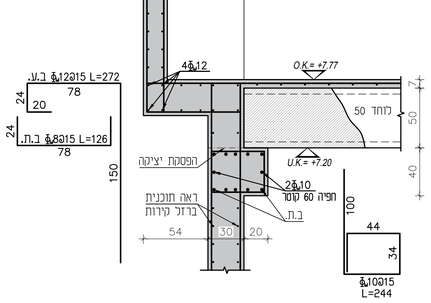

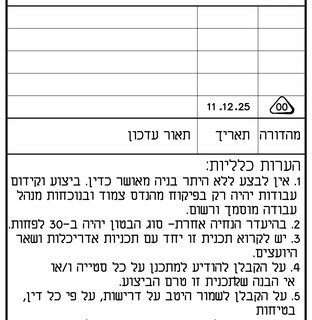

הערות כלליות:

1. אין לבצע כלא היתר בניה מאושר כדין. ביצוע וקידום עבודות יהיה רק בפיקוח מהנדס צמוד ובנוכחות מנהל עבודה מוסמך ורשום.
2. בהיעדר הנחיה אחרת- סוג הבטון יהיה ב-30 לפחות.
3. יש לקרוא תכנית זו יחד עם תכניות אדריכלות ושאר היועצים.
4. על הקבלן להודיע למתכנן על כל סטייה ו/או אי הבנה שתתכנית זו טרם הביצוע.
5. על הקבלן לשמור היטב על דרישות, על פי כל דין, בפיזחות
מזמירות במהלך ביצוע העבודות. אין לבצע הרכבות של אלמנטים ו/או הנפות באזור בו עוברים אנשים. עמדים יתמכו ב-2 כיוונים.
7. יש לבצע בדיקות בטון (לחיצה) על פי דרישות התי"ב- 7, 28, 60 יום, במבני מים יש לקחות דגימות לבדיקות מים ע"פ תי"ב.
8. שרוולים ומעברים יש לקבל מיועצי חשמל, אינס' ומיזוג.
9. שים לב: בכל השטחים הרטובים כגון: מרפסות שמש -חדרים רטובים -חיפויי חוץ -ספים וכו, יש לאטום ע"פ חוק תכנון ובניה.
10. גמר הבטון יהיה לפי תכניות אדריכליות, רצפות בטון יוחלקו בהליקופטר, שכבת שוחקה לפי הנחייה פרטנית של המתכנן והמזמין), גמר רמפות בטון יהיה, בהיעדר הנחייה אחרת, מסורק.
11. יש לתמוך את התקרה באזורים של הטרנספורמציה עד גמר התקשרות הקומה שמעל.
12. עובי כיסוי הבטון ברכיבים הנמצאים מתחת לפני הקרקע יהיה 50 מ"מ.
13. עובי כיסוי הבטון ברכיבים הנמצאים מעל לפני הקרקע יהיה 30 מ"מ.
14. הבטון יתאים לדרגת חשיפה 3 לפי טבלה 3.2 בתי"ת 466 חלק 1.
15. סוג הפלדה: Ø – תי"ת 4466 חלק 3.
– תי"ת 4466 חלק 4.
16. התכניות לביצוע לאחר אישור אדריכל ויועץ קרקע.

מצבעם אחראי לבדיקת המידות ולהתאמתן במקום.
על המבצע לבקר את כל המידות ועל כל סטיות או אי התאמה יודיע למתכנן.
אין לבצע מידות ע"פ מדידה מהשרטוט.

מקרא:

בטון ממשיך	
בטון מפסיק	
בטון צומח	
זחתך מקומי	

הפצה:

שם	תאריך

שינויים:

00	11.12.25	

מהדורה	תאריך	תאור עדכון

הרזם
עמותת צרכי הרבים רצופות

אדריכלות
איבגי קרמן אדריכלות

שם הפרויקט:
בית כנסת הרמב"ם מודיעין עילית

שם התכנית:
קומה 1 תבנית

סטטוס:	לעיון ○	לאישור ○	נמכרז ●	לביצוע ○

מהדורה:	תאריך:
00	11.12.2025

שם קובץ:	100-GWE-110	קנ"מ: 1:50 1:25
מס' גליון:	100-GWE-110-00	מס' סידורי: 000

פוליגון הנדסה
תכנון יישוב ופיקוח