המבצע אחראי לבדיקת המידות ולהתאמתן במקום.
על המבצע לבקר את כל המידות ועל כל טעות או אי התאמה יודיע למתכנן.
אין לבצע מידות ע"פ מדידה מהשרטוט.

מקרא:

| | |
|---|---|
| בטון ממשיך | ▨ |
| בטון מפסיק | ▩ |
| בטון צומח | ▨ |
| חתך מקומי | ▒ |

הפצה:

| שם | תאריך | |
|---|---|---|
| | | |
| | | |
| | | |
| | | |
| | | |

שינויים:

| | | |
|---|---|---|
| | | |
| | | |
| | | |
| | | |
| 00 | 11.12.25 | |
| מהדורה | תאריך | תאור עדכון |

## הערות כלליות:

1. אין לבצע ללא היתר בניה מאושר כדין. ביצוע וקידום עבודות יהיה רק בפיקוח מהנדס צמוד ובנוכחות מנהל עבודה מוסמך ורשום.
2. בהיעדר הנחיה אחרת- סוג הבטון יהיה ב-30 לפחות.
3. יש לקרוא תכנית זו יחד עם תכניות אדריכלות ושאר היועצים.
4. על הקבלן להודיע למתכנן על כל סטייה ו/או אי הבנה שבתכנית זו טרם הביצוע.
5. על הקבלן לשמור היטב על דרישות, על פי כל דין, בטיחות מחמירות במהלך ביצוע העבודות. אין לבצע הרכבות של אלמנטים ו/או הנפות באזור בו עוברים אנשים. עמודים יתמכו ב-2 כיוונים.
7. יש לבצע בדיקות בטון (לחיצה) על פי דרישות הת"י ב- 7, 28, 60 יום, במבני מים יש לקחת דגימות לבדיקות מים ע"פ ת"י.
8. שרוולים ומעברים יש לקבל מיועצי חשמל, אינס' ומיזוג.
9. שים לב: בכל השטחים הרטובים כגון: מרפסות שמש -חדרים רטובים -חיפויי חוץ -ספים וכו, יש לאטום ע"פ חוק תכנון ובניה.
10. גמר הבטון יהיה לפי תכניות אדריכליות, רצפות בטון יוחלקו בהליקופטר, שכבת שחיקה לפי הנחייה פרטנית של המתכנן והמזמין, גמר רמפות בטון יהיה, בהיעדר הנחייה אחרת, מסורק.
11. יש לתמוך את התקרה באזורים של הטרנספורמציה עד גמר התקשות הקומה שמעל.
12. עובי כיסוי הבטון ברכיבים הנמצאים מתחת לפני הקרקע יהיה 50 מ"מ.
13. עובי כיסוי הבטון ברכיבים הנמצאים מעל לפני הקרקע יהיה 30 מ"מ.
14. הבטון יתאים לדרגת חשיפה 3 לפי טבלה 3.2 בת"י 466 חלק 1.
15. סוג הפלדה: $\Phi_w$ – ת"י 4466 חלק 3.
    Ŧ – ת"י 4466 חלק 4.
16. התכניות לביצוע לאחר אישור אדריכל ויועץ קרקע.

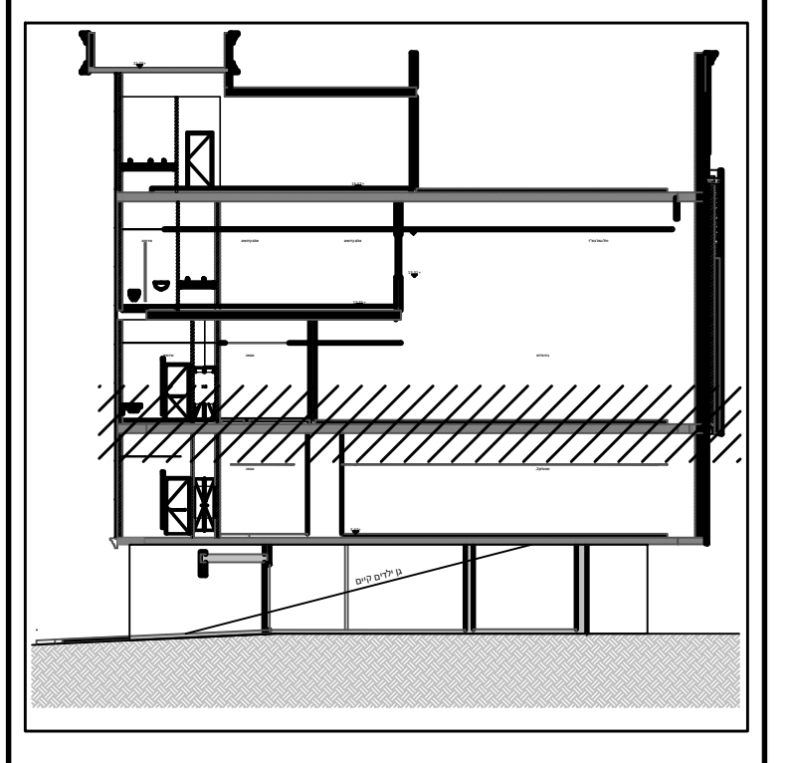

היזם

**עמותת צרכי הרבים רצופות**

אדריכלות

**איבגי קרמן אדריכלות**

שם הפרויקט :

בית כנסת הרמב"ם
מודיעין עילית

שם התכנית :

קומה 1
תוכנית ברזל

| סטטוס: | לעיון ○ | לאישור ○ | למכרז ● | לביצוע ○ |
|---|---|---|---|---|
| מהדורה: | 00 | תאריך: | 11.12.2025 | |
| שם קובץ: | 100-GWE-110 | קנ"מ: | 1:25 1:50 | |
| מס' גליון: | 100-GWE-110-rs-00 | מס' סידורי: | 000 | |

פוליגון הנדסה
תכנון ייעוץ ופיקוח

## ברזל תחתון
1:50

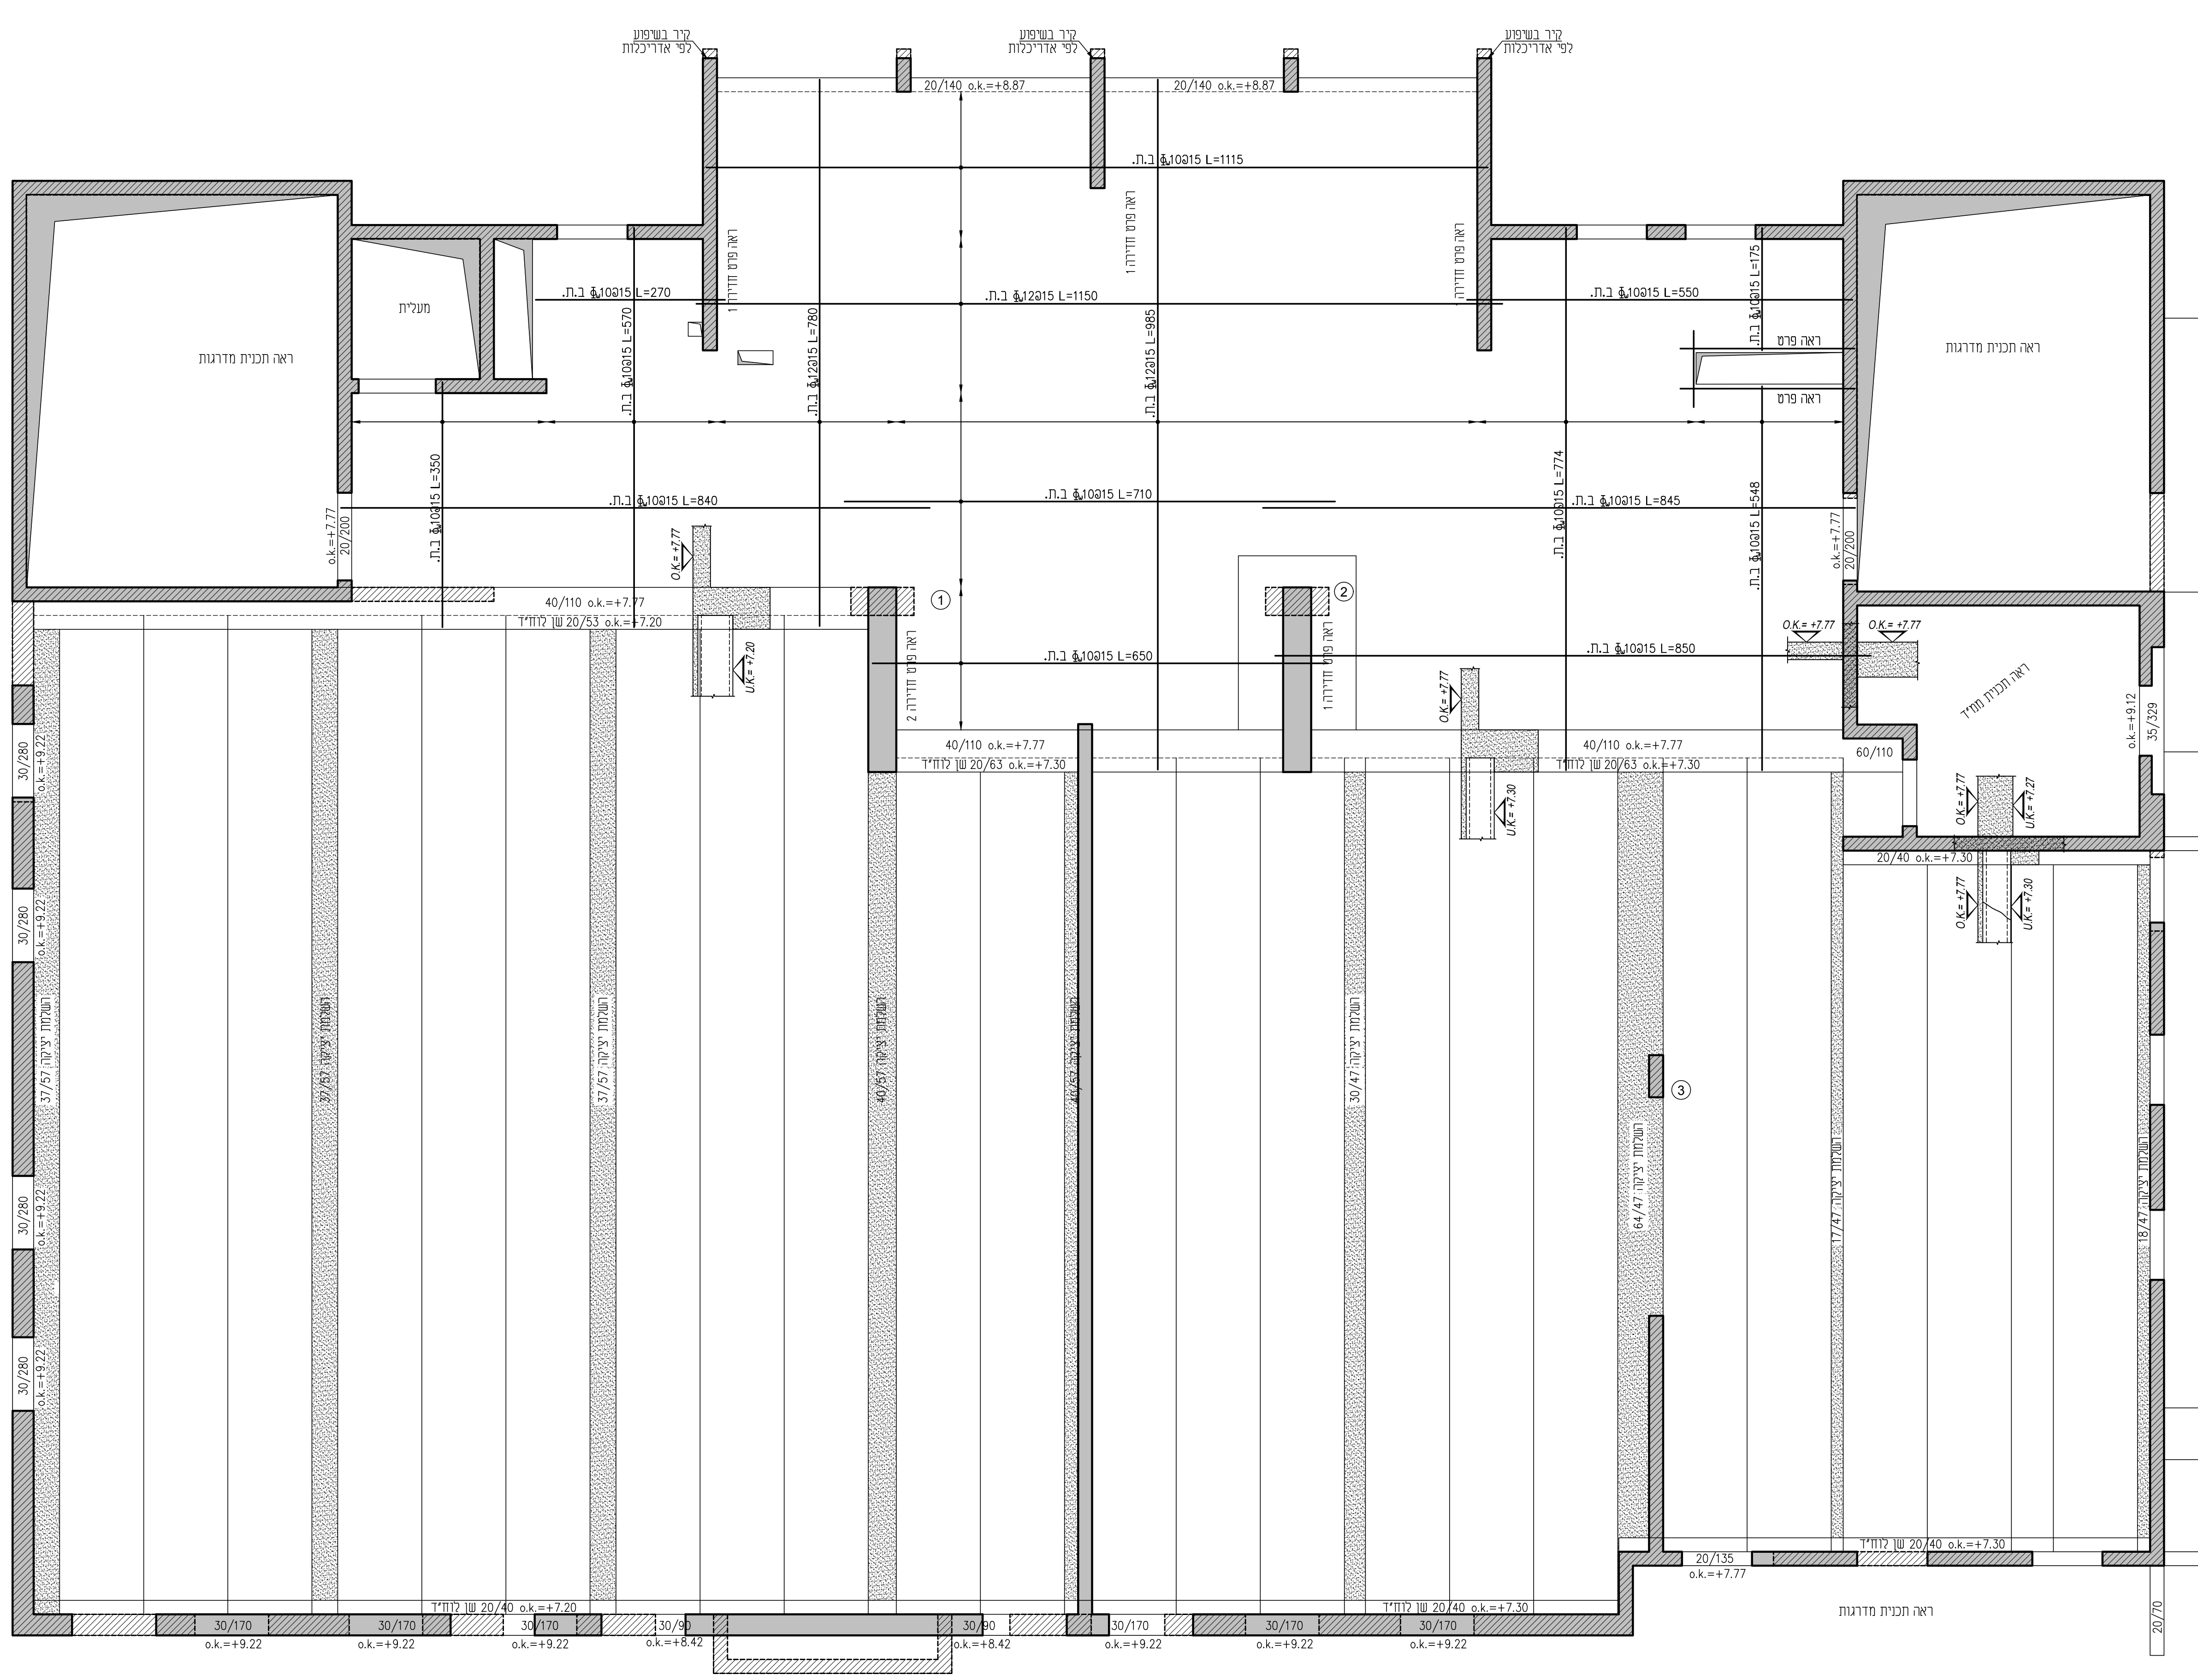

## ברזל עליון וקורות
1:50

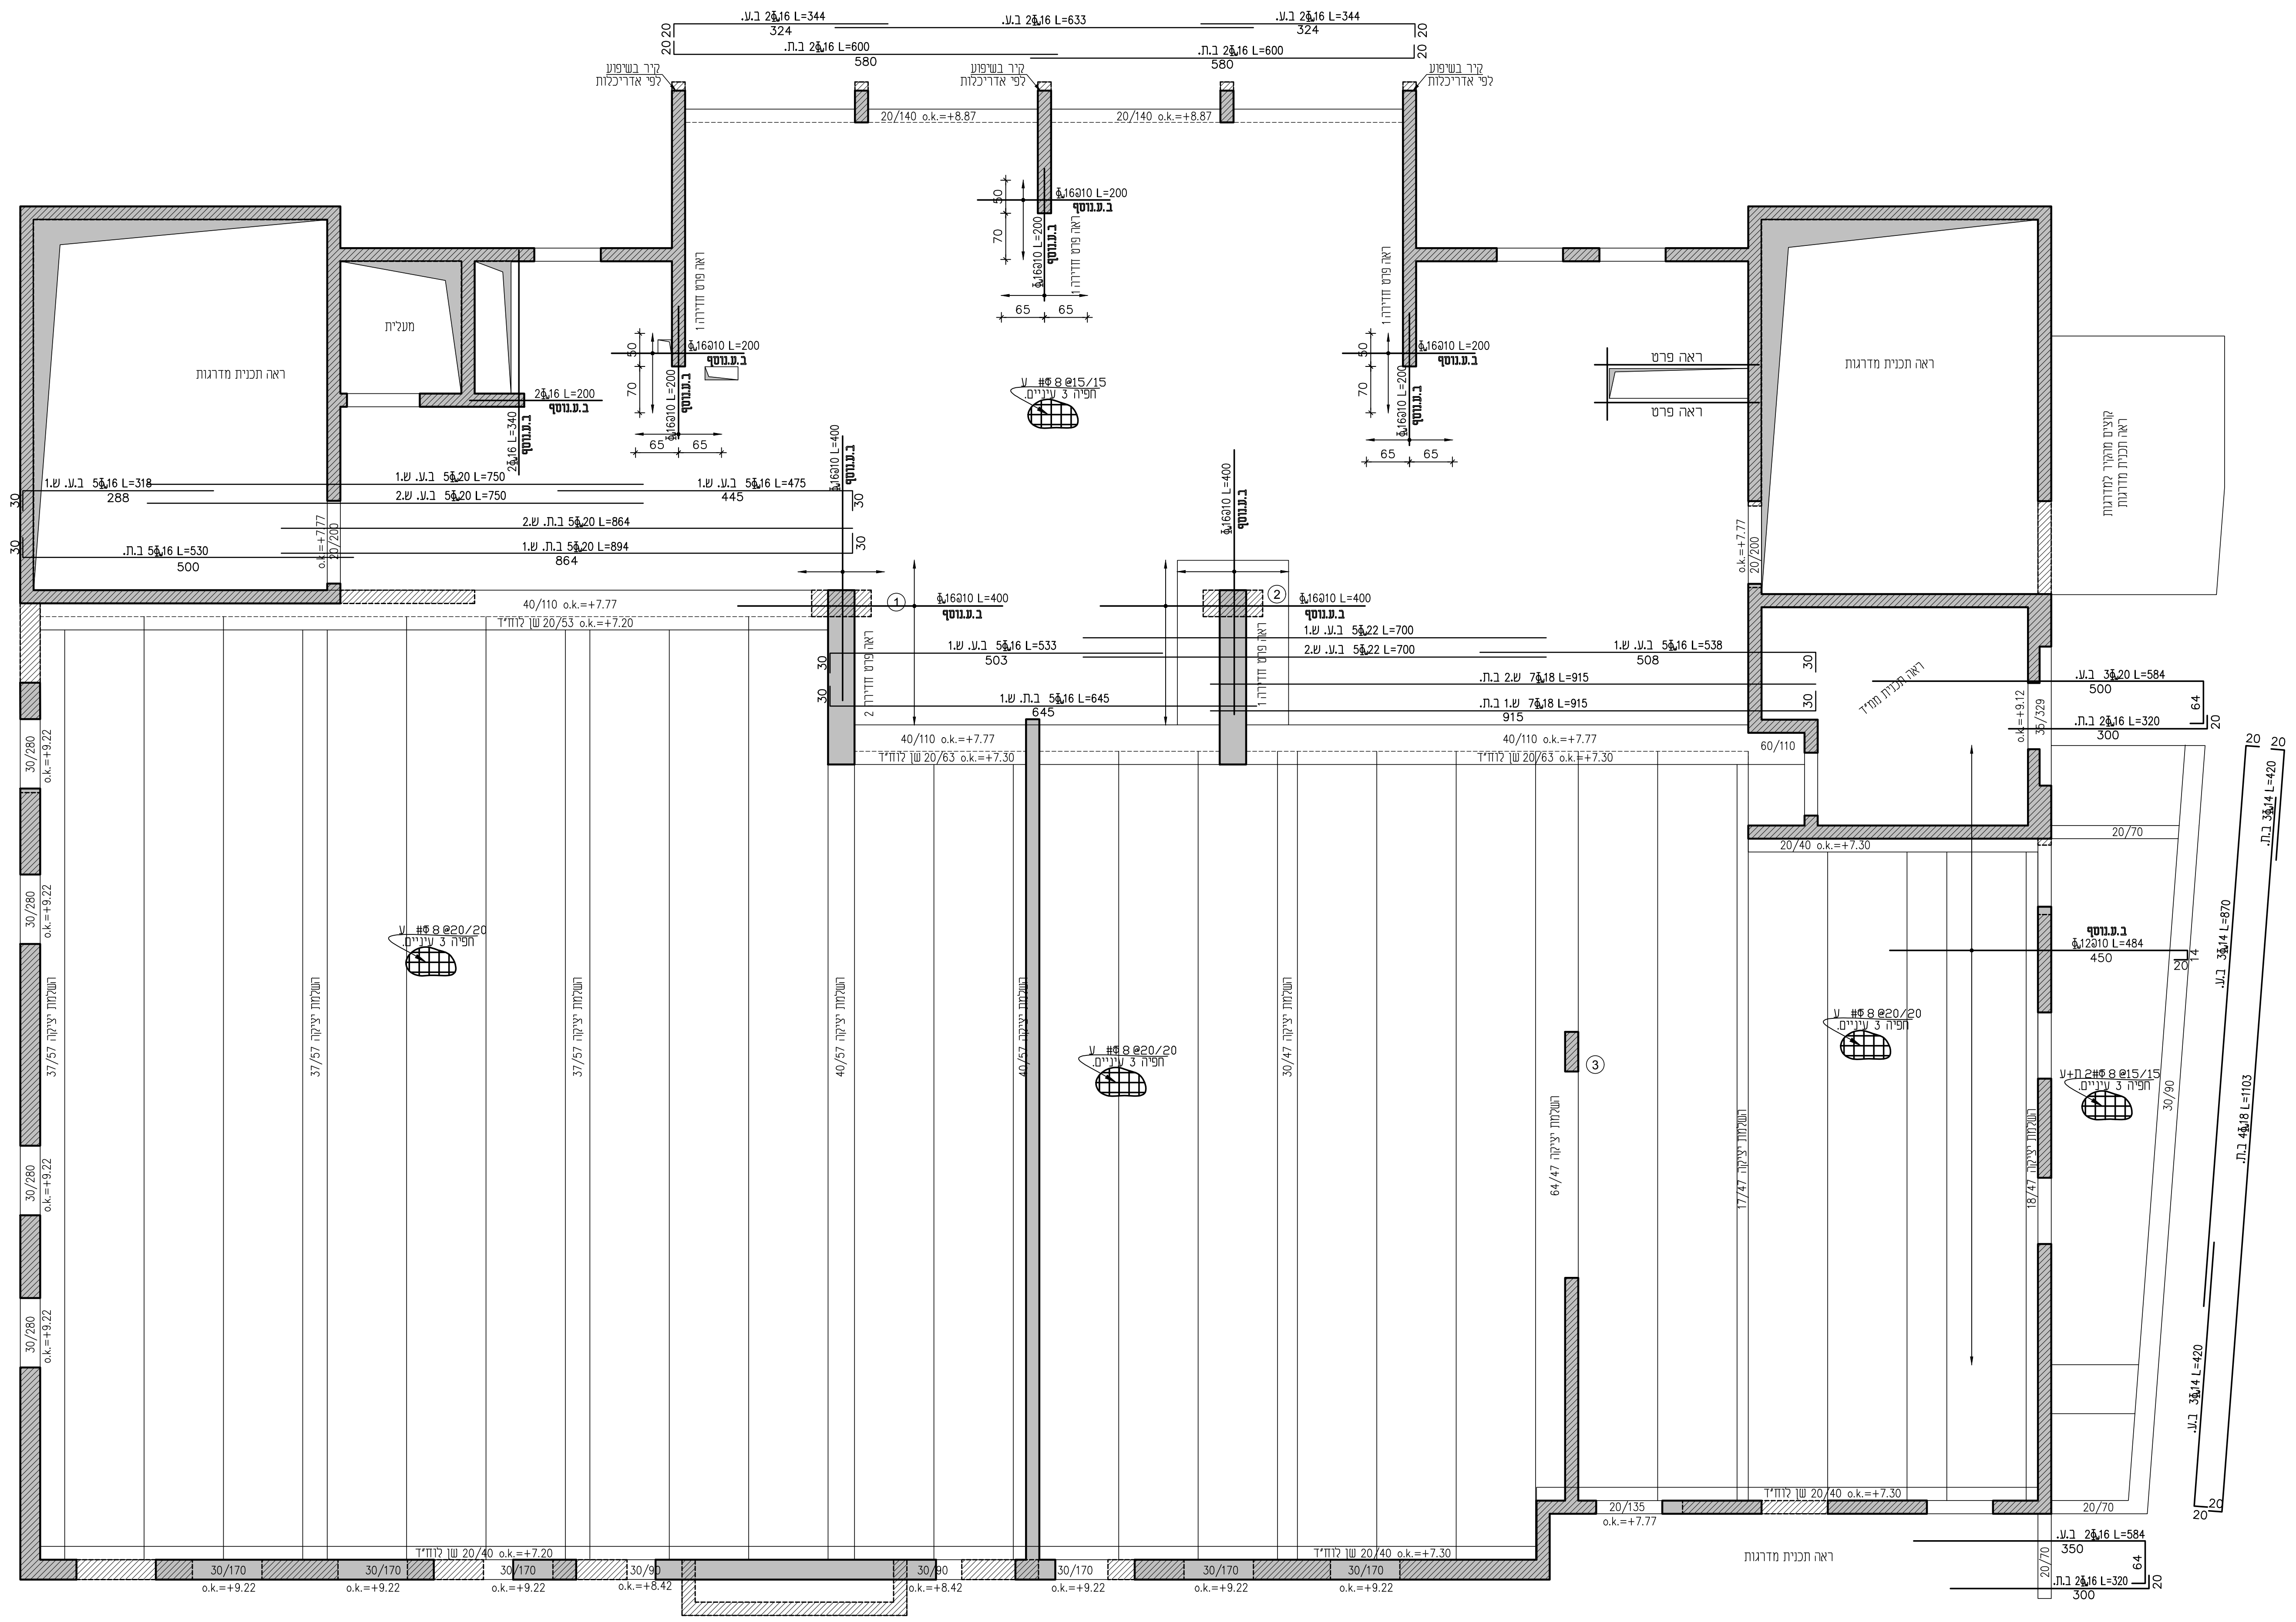

### פרט זיון מסביב לפתח ברצפה,בתנאי שלא צוין אחרת
1 : 25

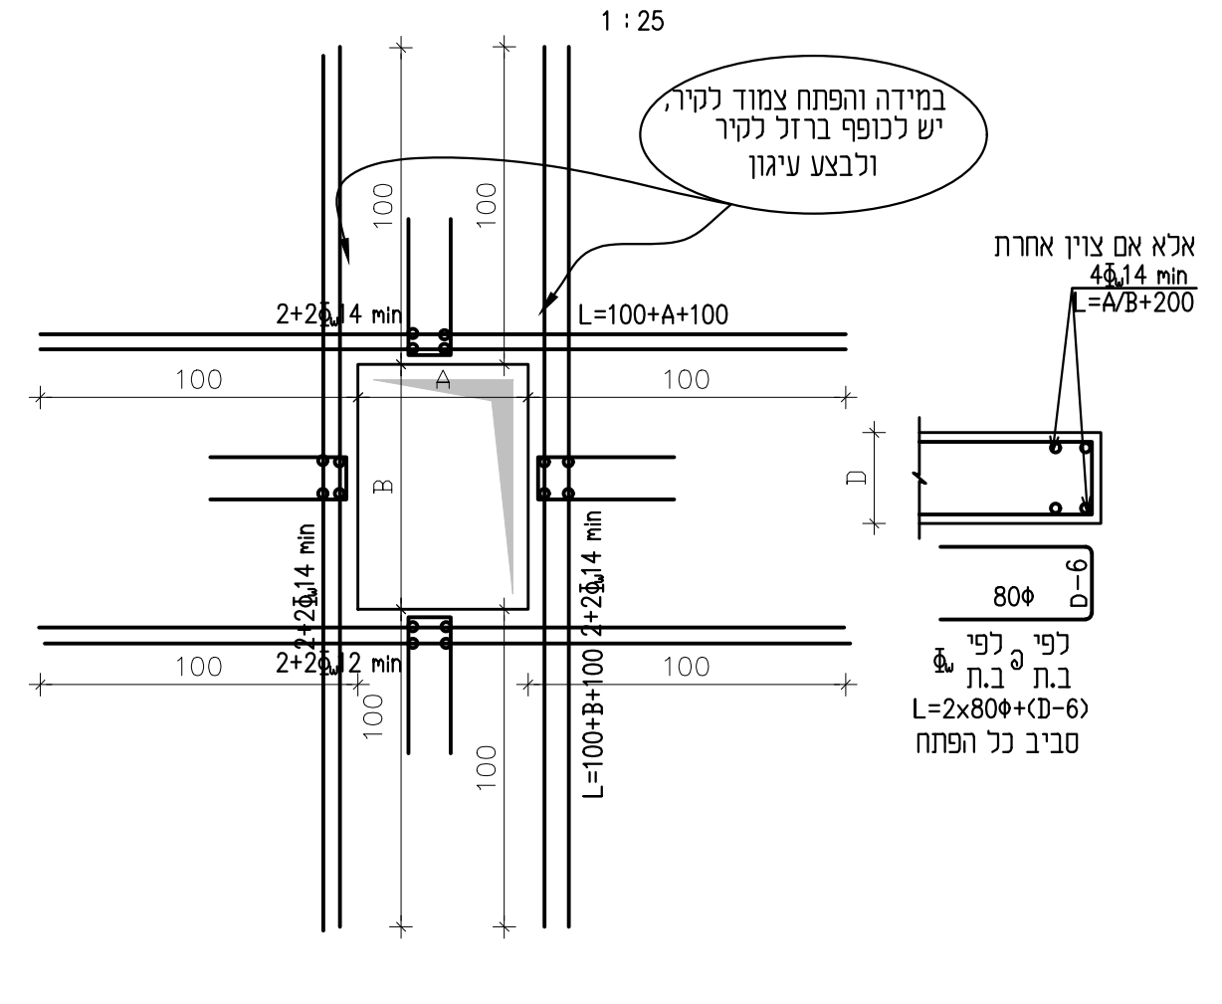

### פרט קצה תקרה ללא קורה
1:25

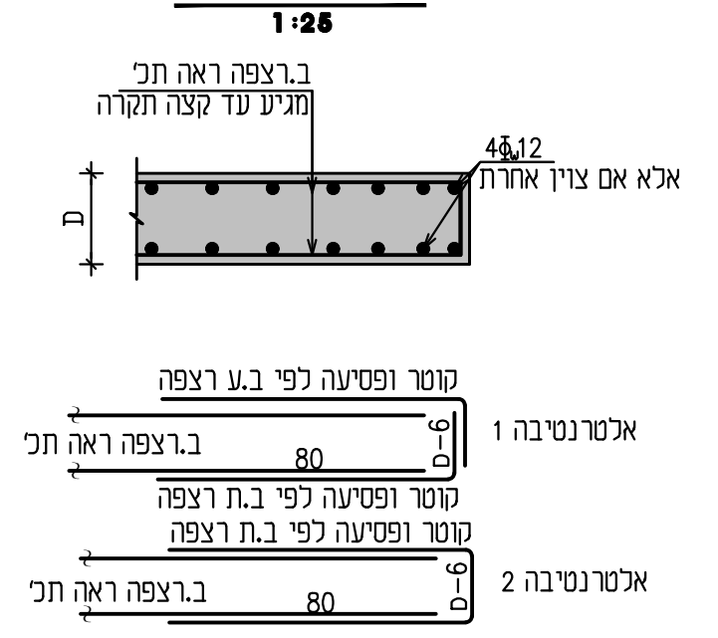

### פרט קצה תקרה עם קורה עולה
1:25

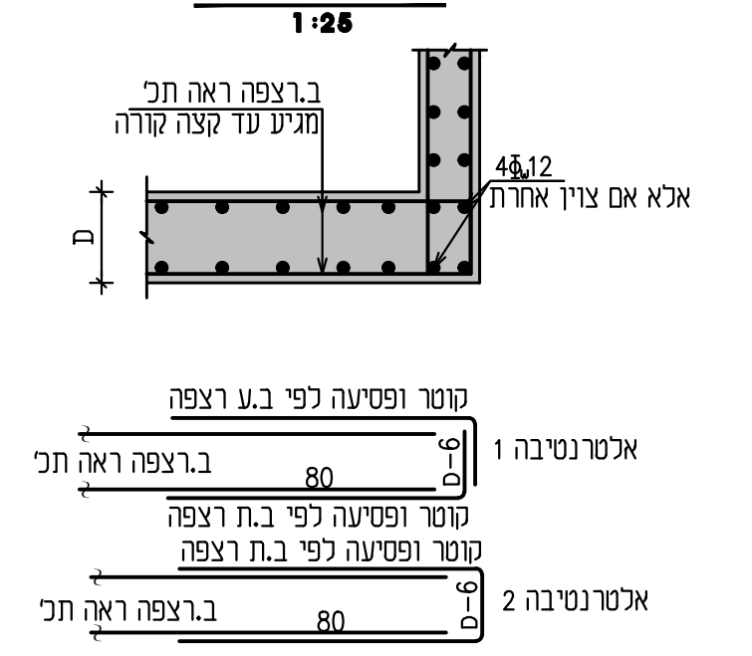

### פרט קצה תקרה עם קורה יורדת
1:25

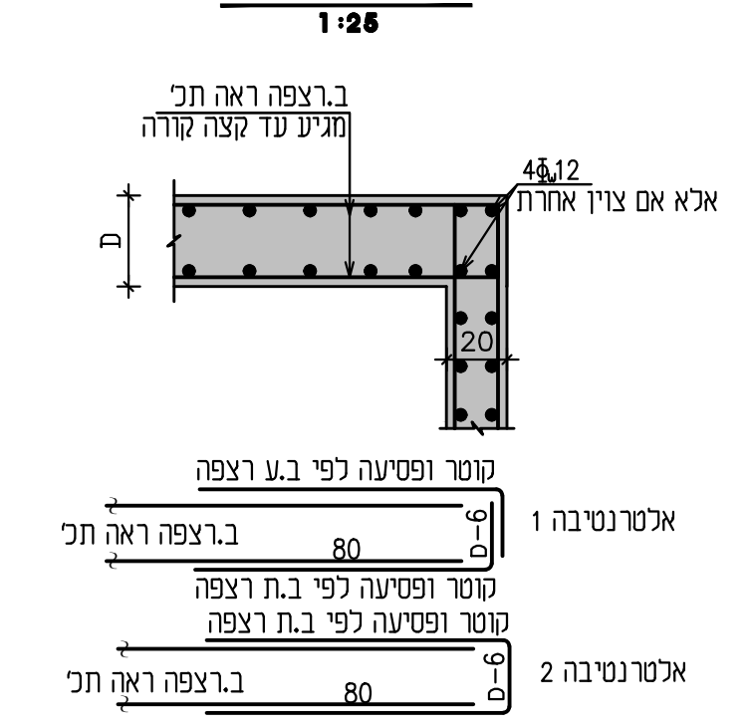

### חתך 1-1
1:25

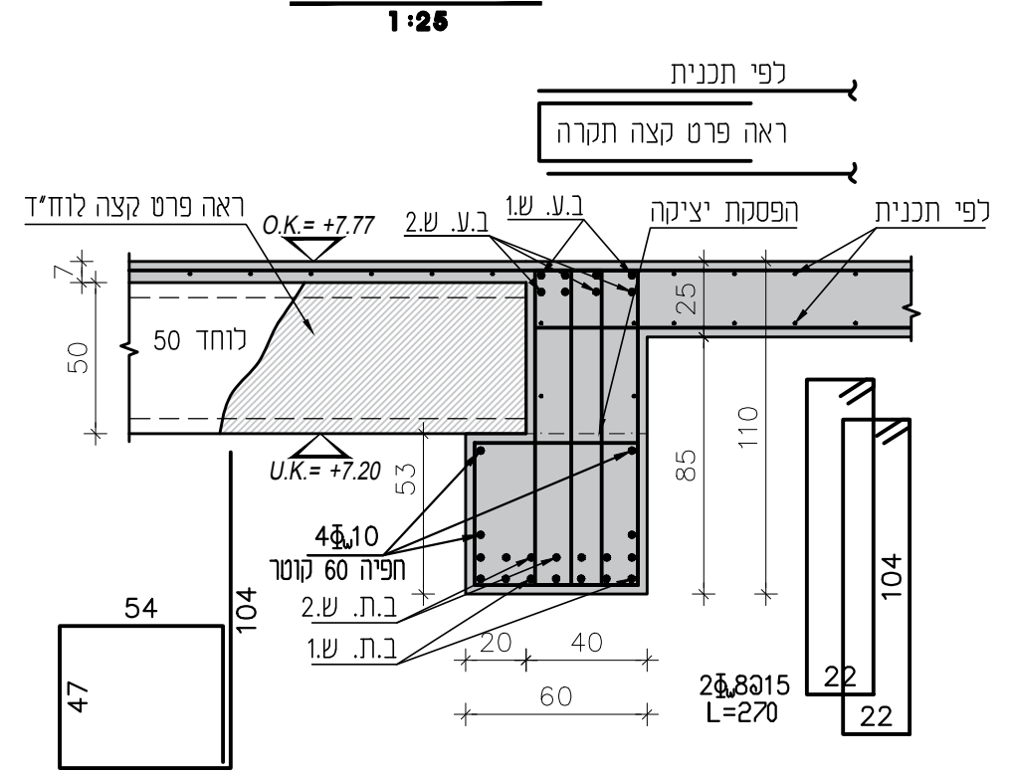

### חתך 2-2
1:25

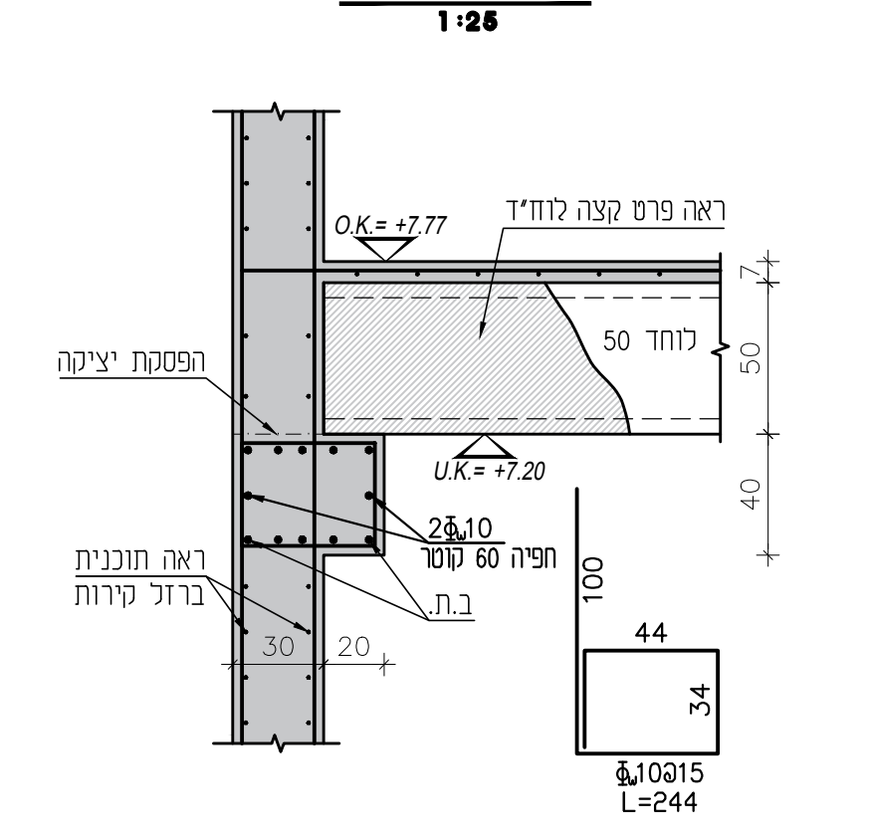

### חתך 3-3
1:25

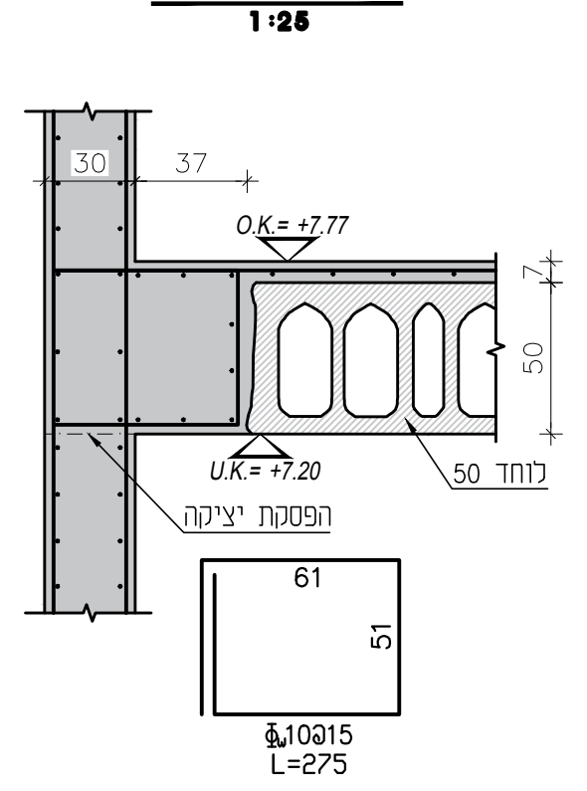

### חתך 4-4
1:25

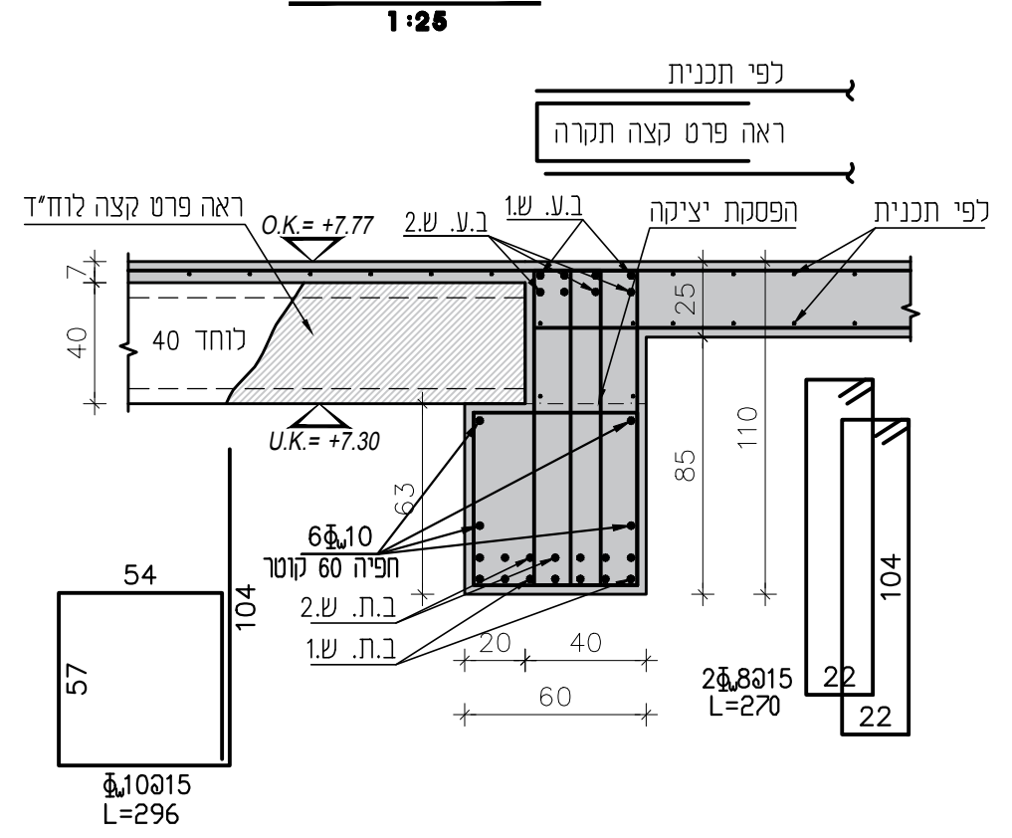

### חתך 5-5
1:25

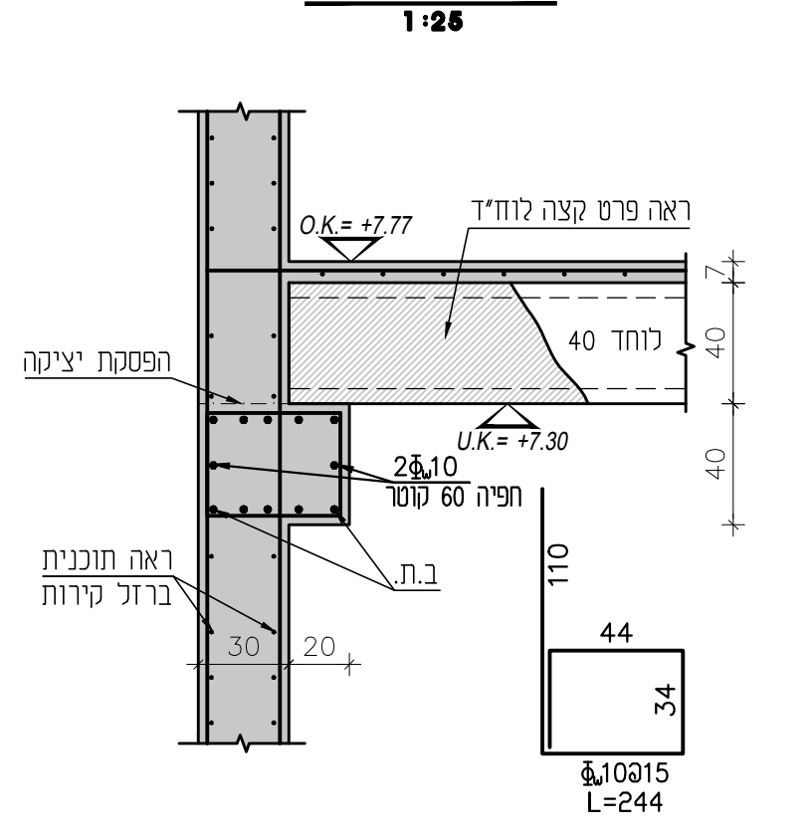

### חתך 6-6
1:25

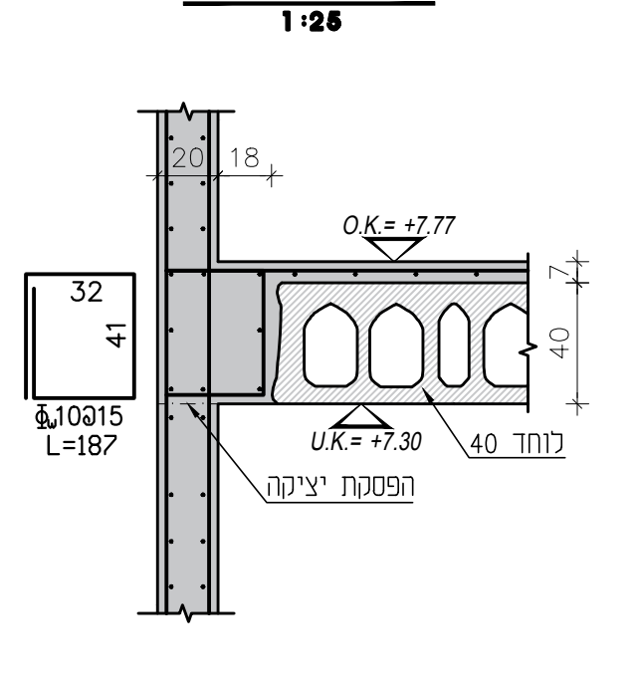

### פרט כללי להוצאת קוצים מקיר\עמוד
1:25

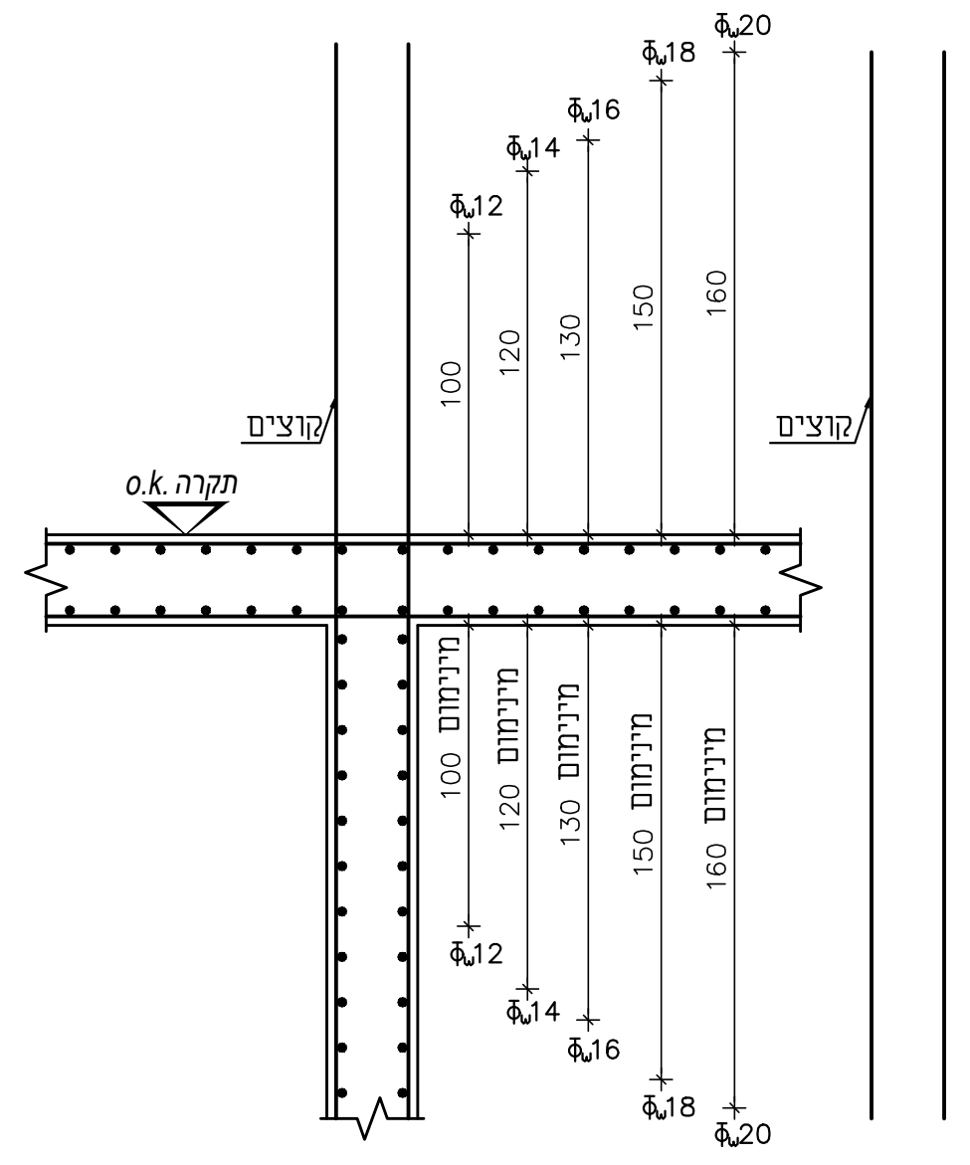

### פרט סידור רשתות מרותכות עקרוני

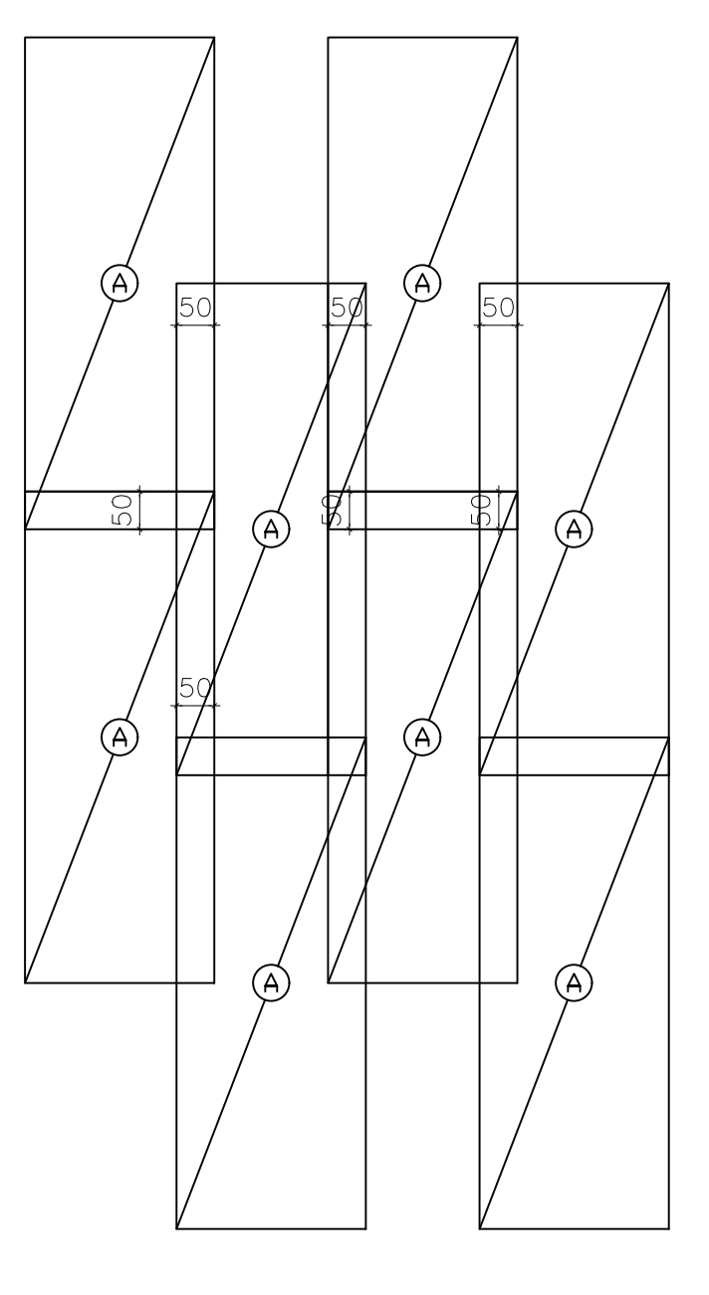

### פרט כללי להוצאת קוצים מרצפה
1:25

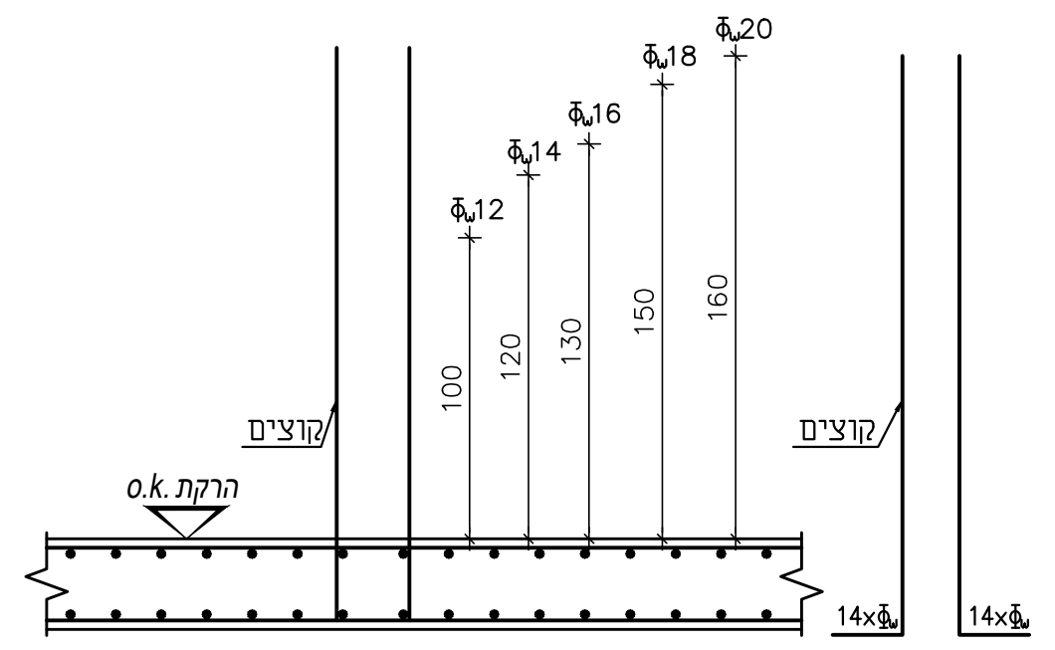

### חתך 11-11
1:25

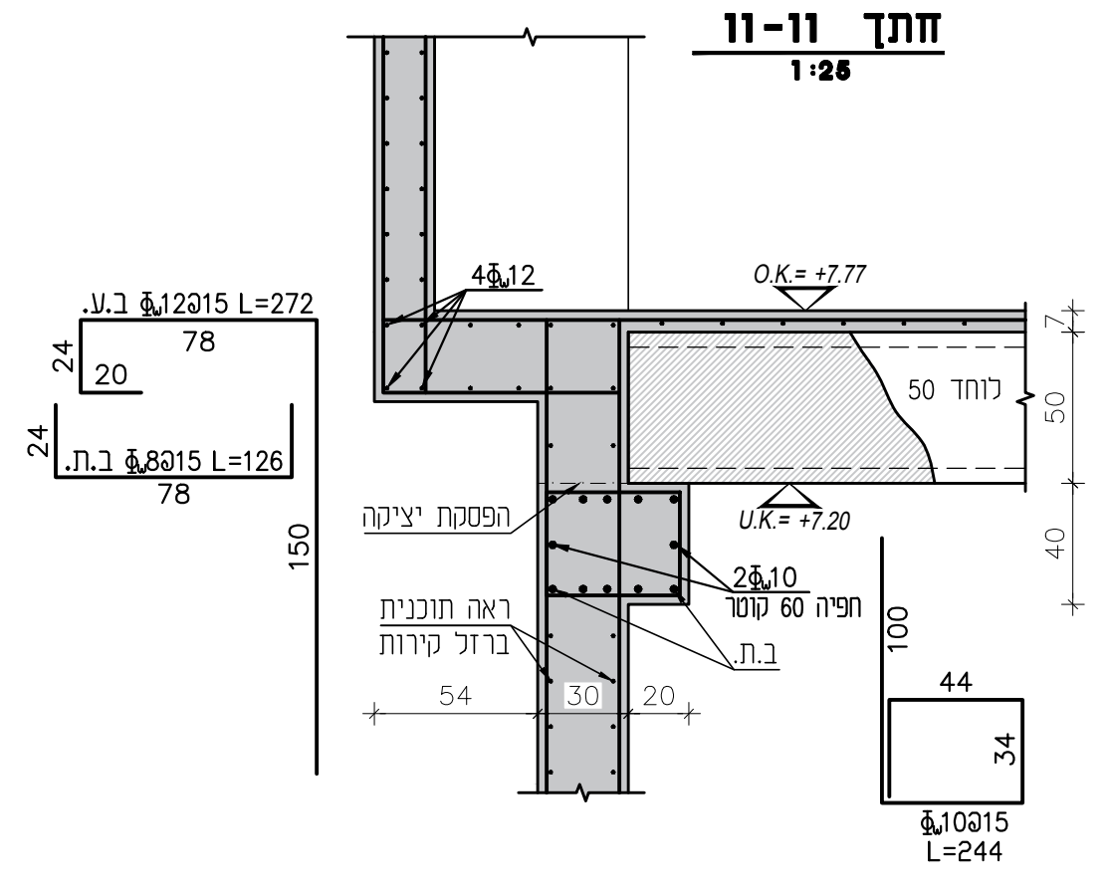

### חתך 10-10
1:25

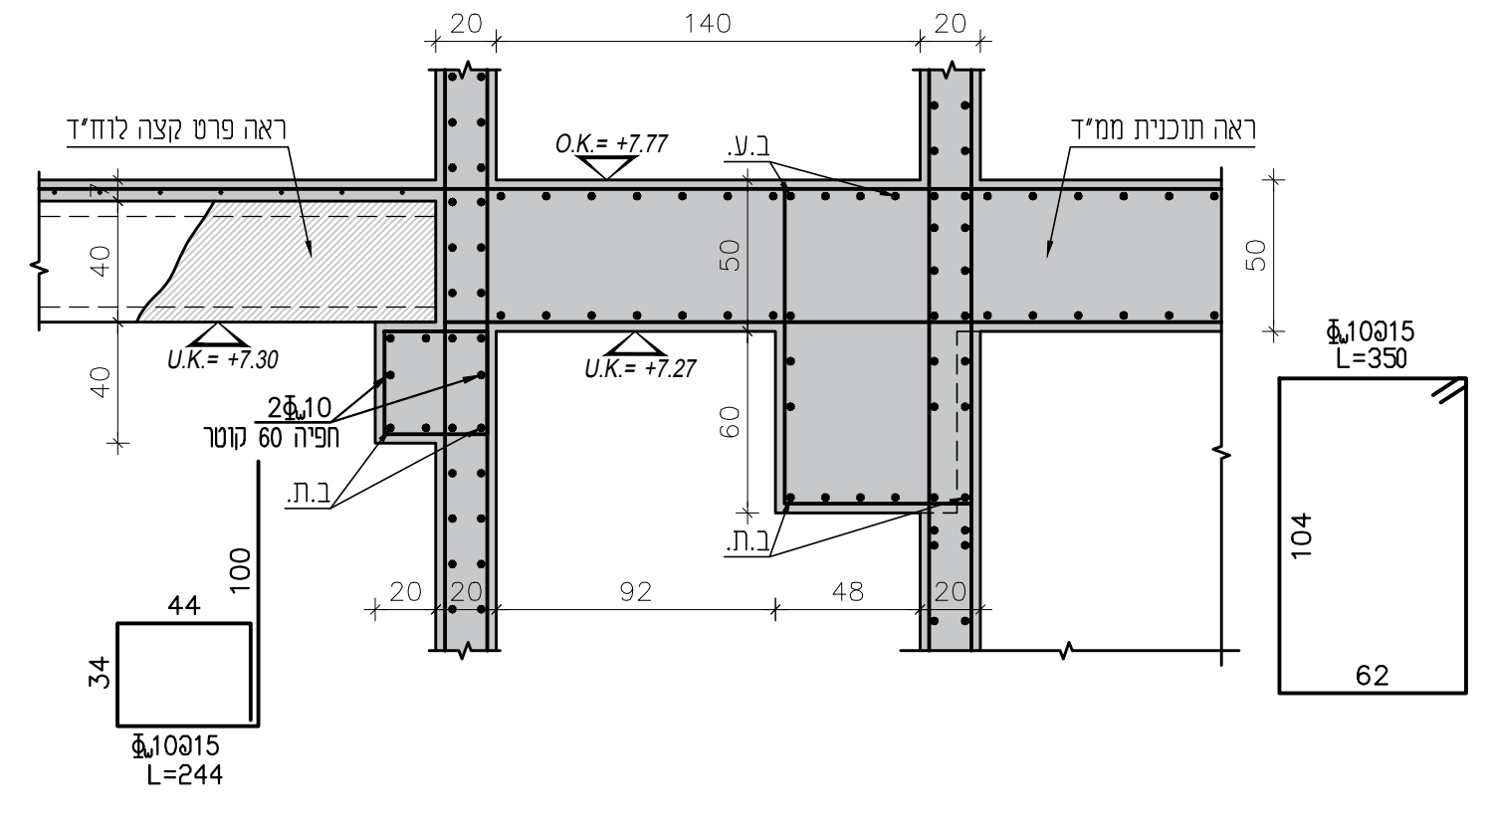

### חתך 8-8
1:25

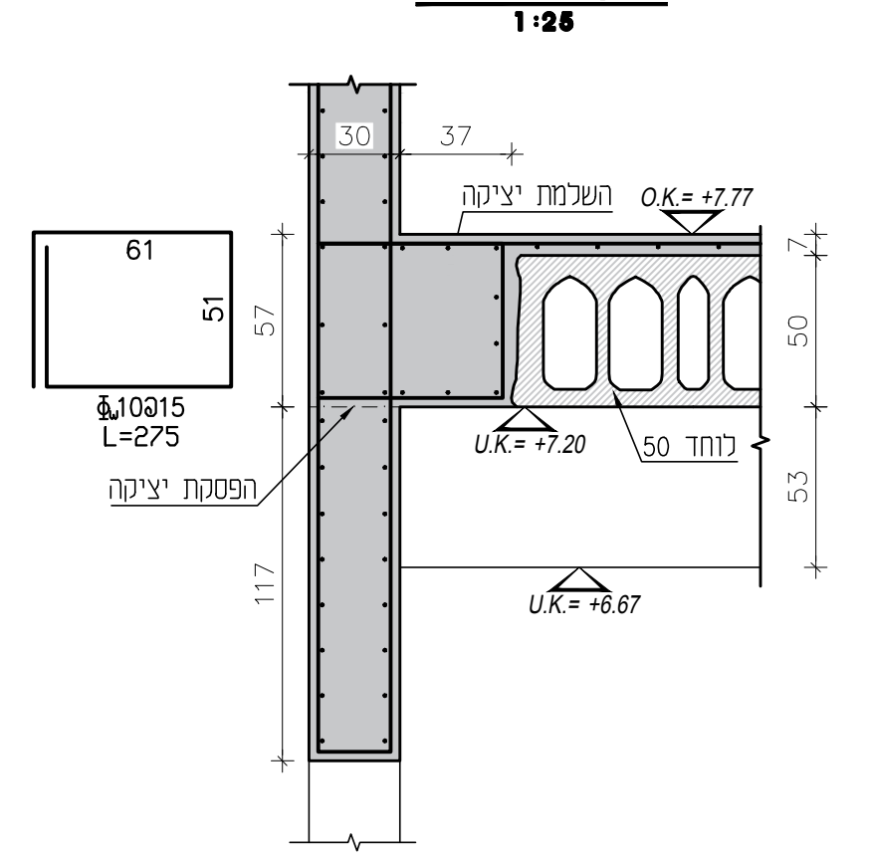

### חתך 7-7
1:25

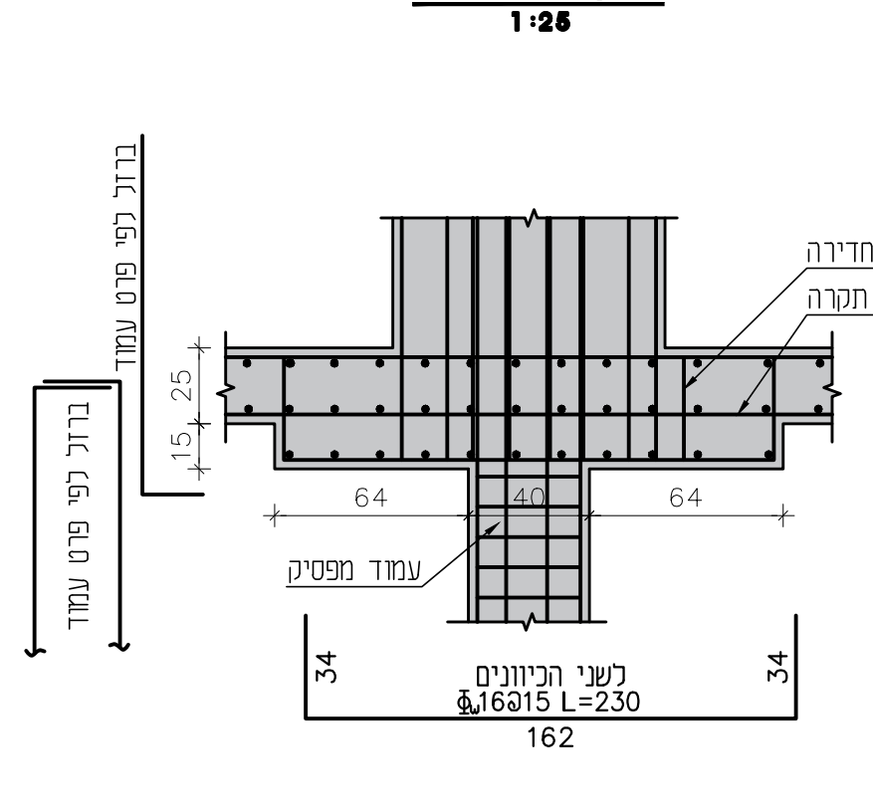

### פרט השלמת יציקה טיפוסי
1:25

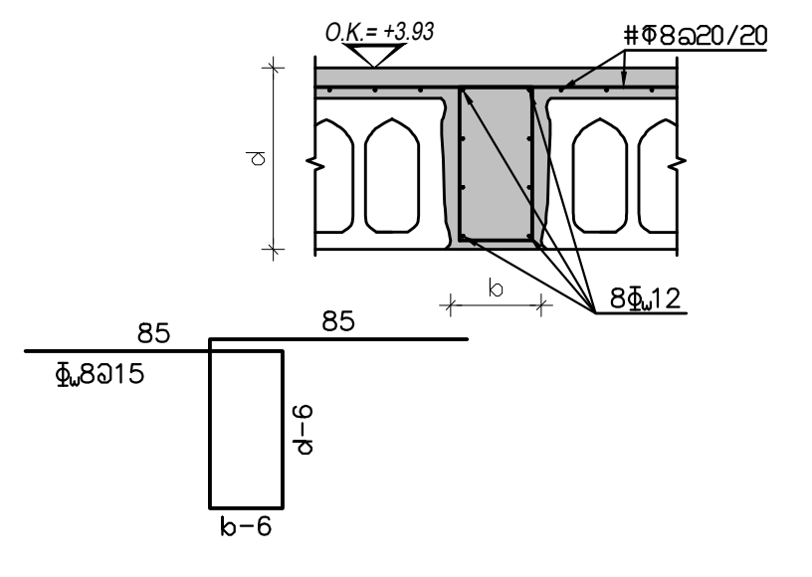

### פרט קצה לוח"ד
1:25

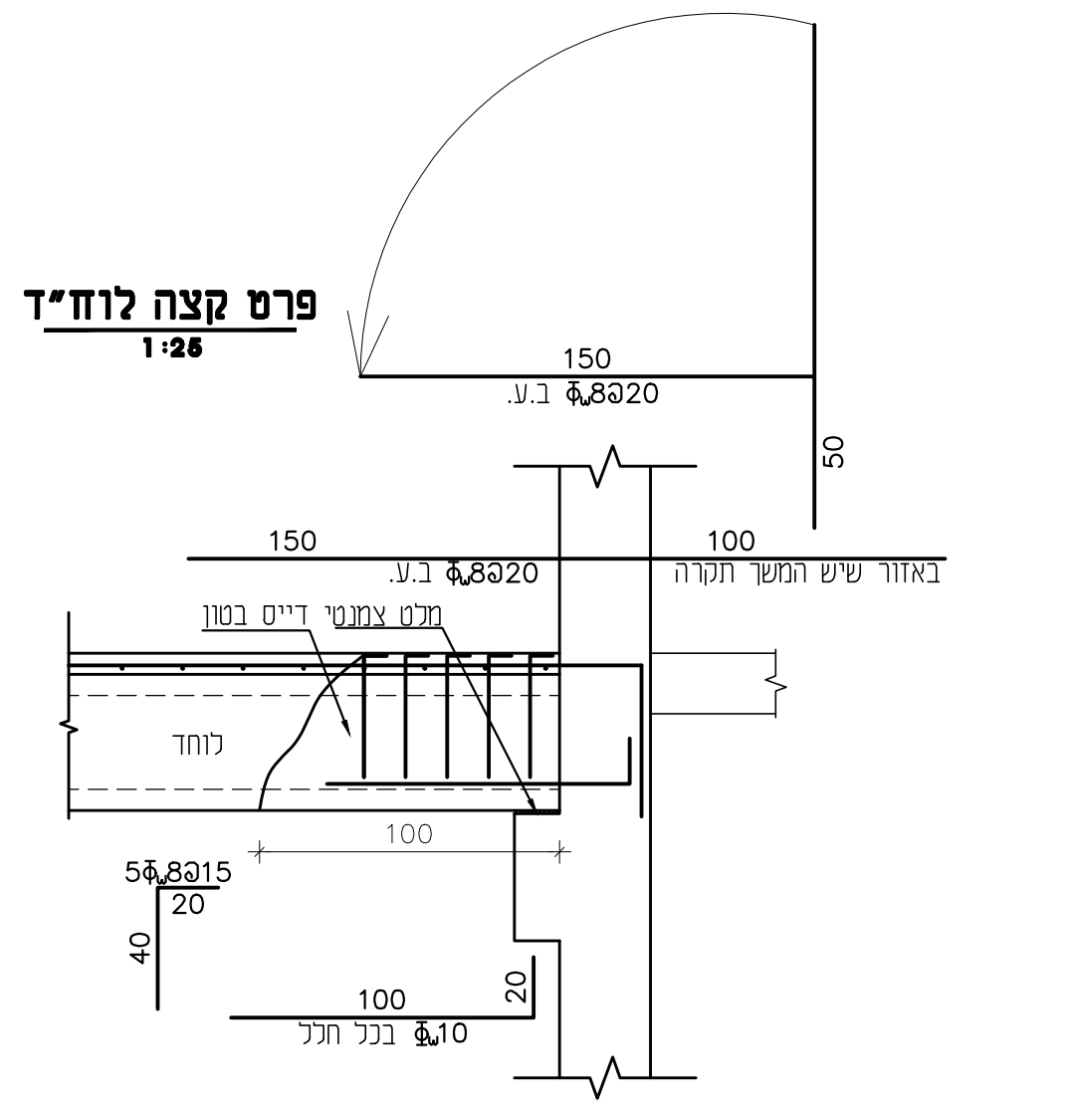

### פרט חדירה 2
1:25
(פינת קיר)

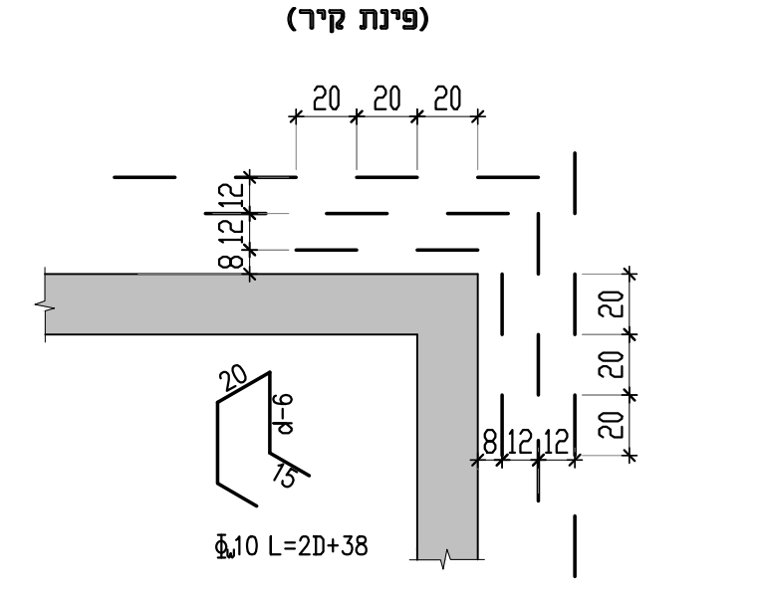

### פרט חדירה 1
1:25
(קצה קיר)